



COUNTRY SIDE — KHAL

Earthen closure — trapezoidal

Dewatering

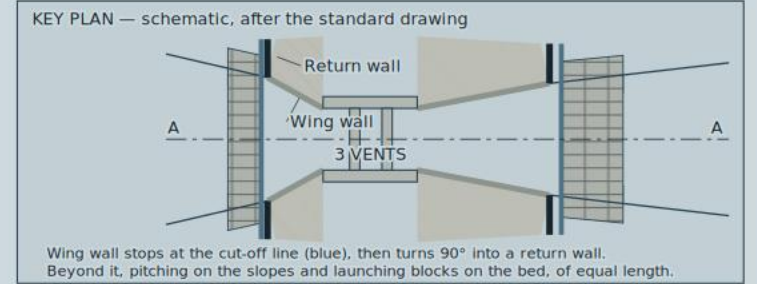

RIVER SIDE — TIDAL

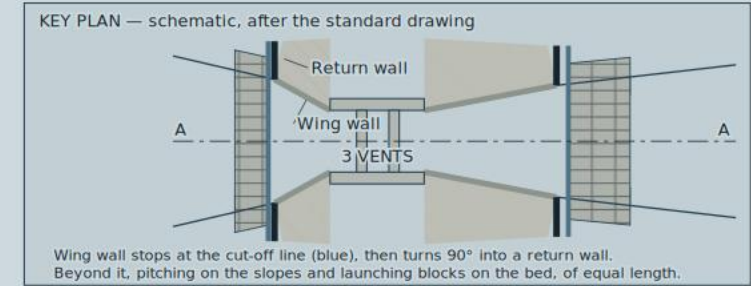

COUNTRY SIDE — KHAL

RIVER SIDE — TIDAL

Earthen closure — trapezoidal

Dewatering

Excavated to Foundation Level

COUNTRY SIDE — KHAL


RIVER SIDE — TIDAL

Earthen closure — trapezoidal



Dewatering

Excavated to Foundation Level

Bearing piles — round, driven, deeper than the cut-off

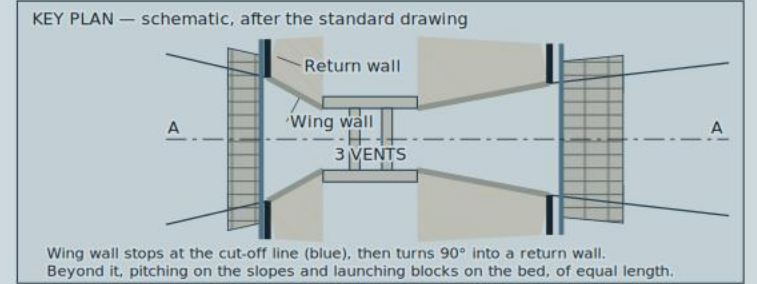


Prepared by: Engr. Arup Chakraborty, Executive Engineer (Civil), Engineering Academy, BPDB-BWDB, Kaptai

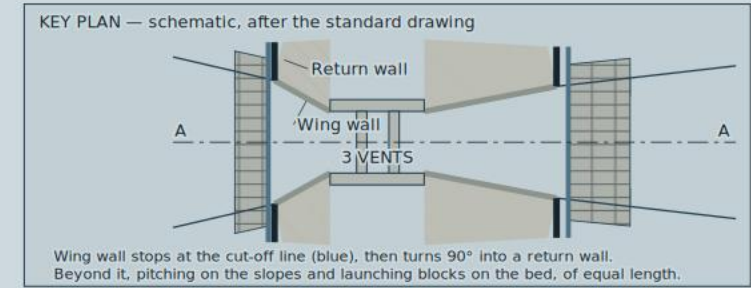
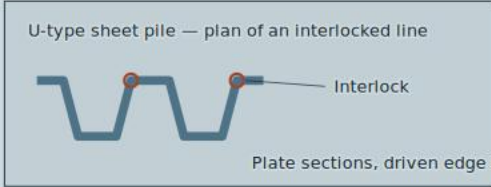


COUNTRY SIDE — KHAL

RIVER SIDE — TIDAL

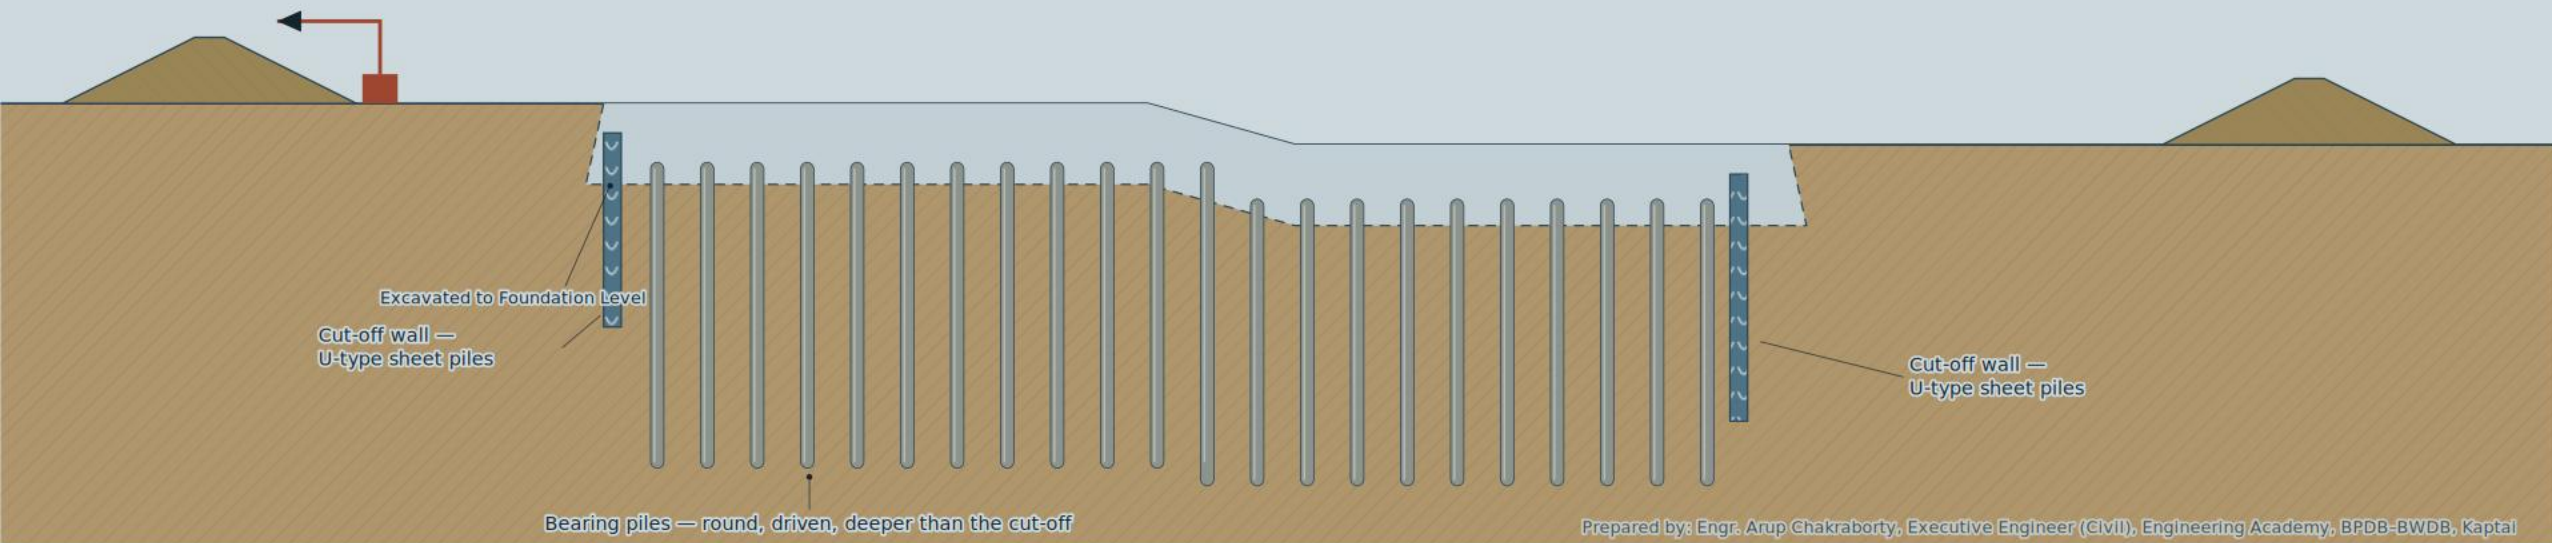


Prepared by: Engr. Arup Chakraborty, Executive Engineer (Civil), Engineering Academy, BPDB-BWDB, Kaptai

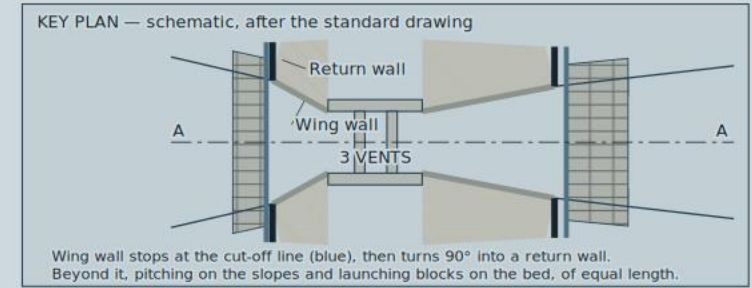
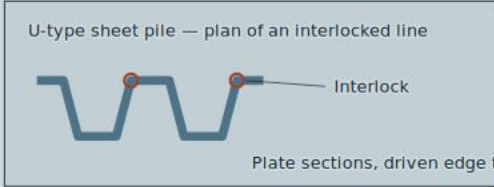


COUNTRY SIDE — KHAL

RIVER SIDE — TIDAL

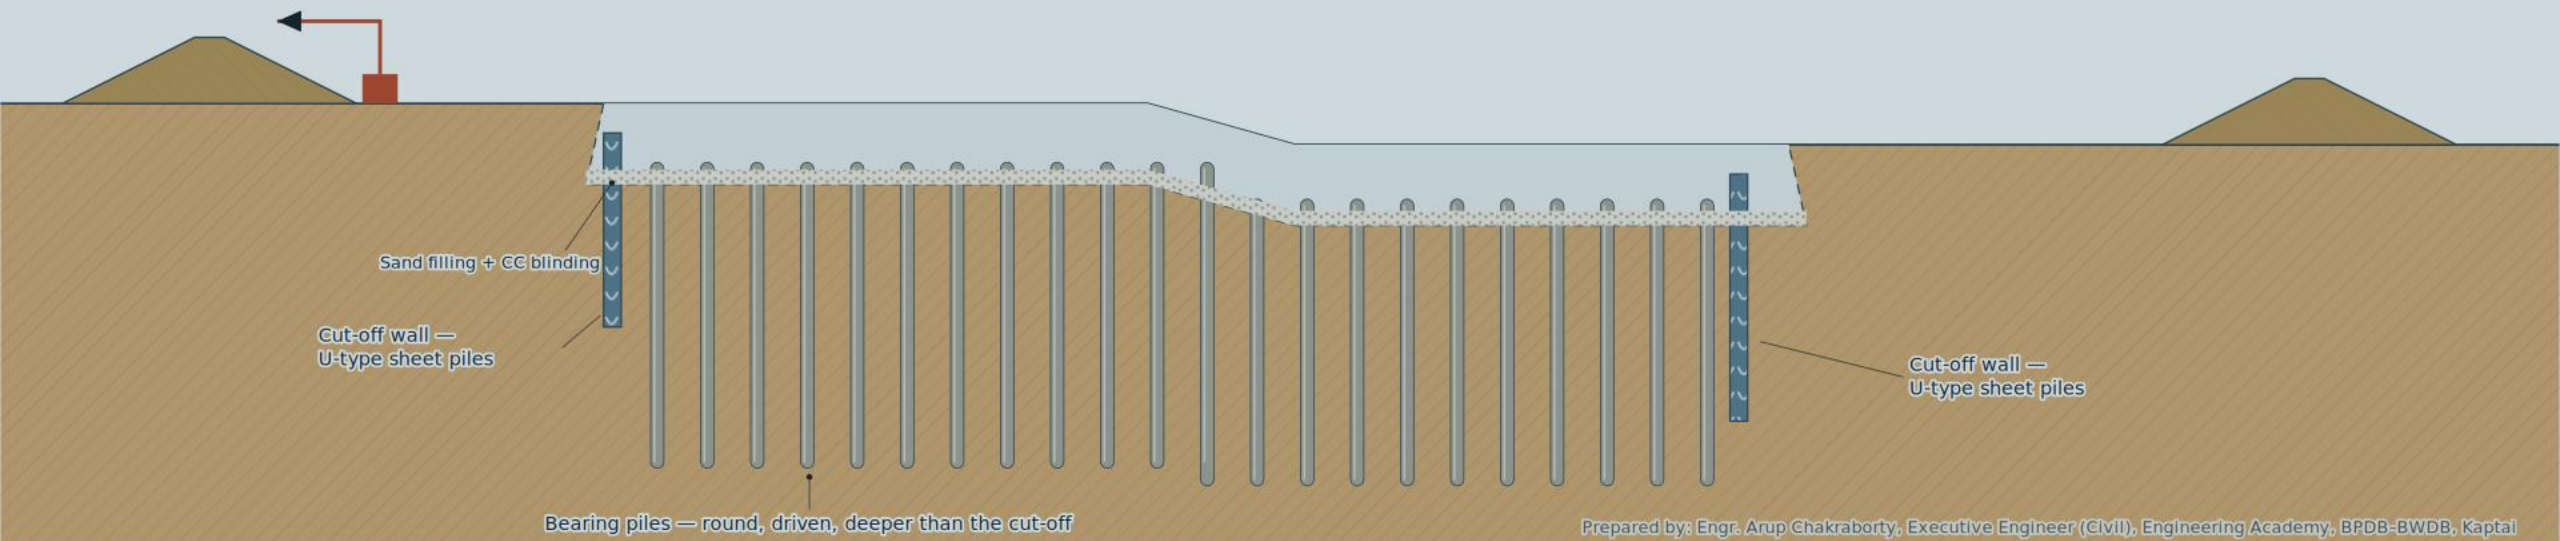


Prepared by: Engr. Arup Chakraborty, Executive Engineer (Civil), Engineering Academy, BPDB-BWDB, Kaptai

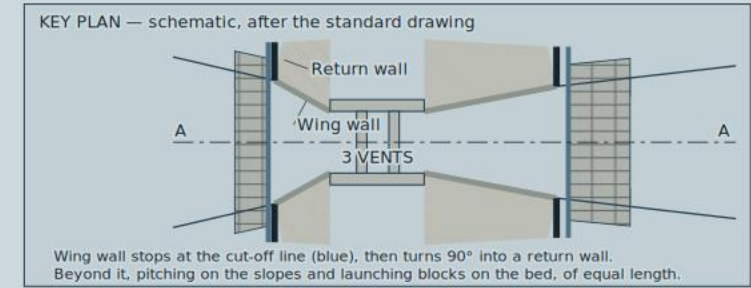
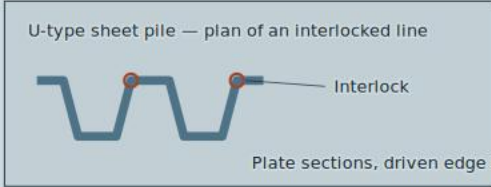



COUNTRY SIDE — KHAL


RIVER SIDE — TIDAL

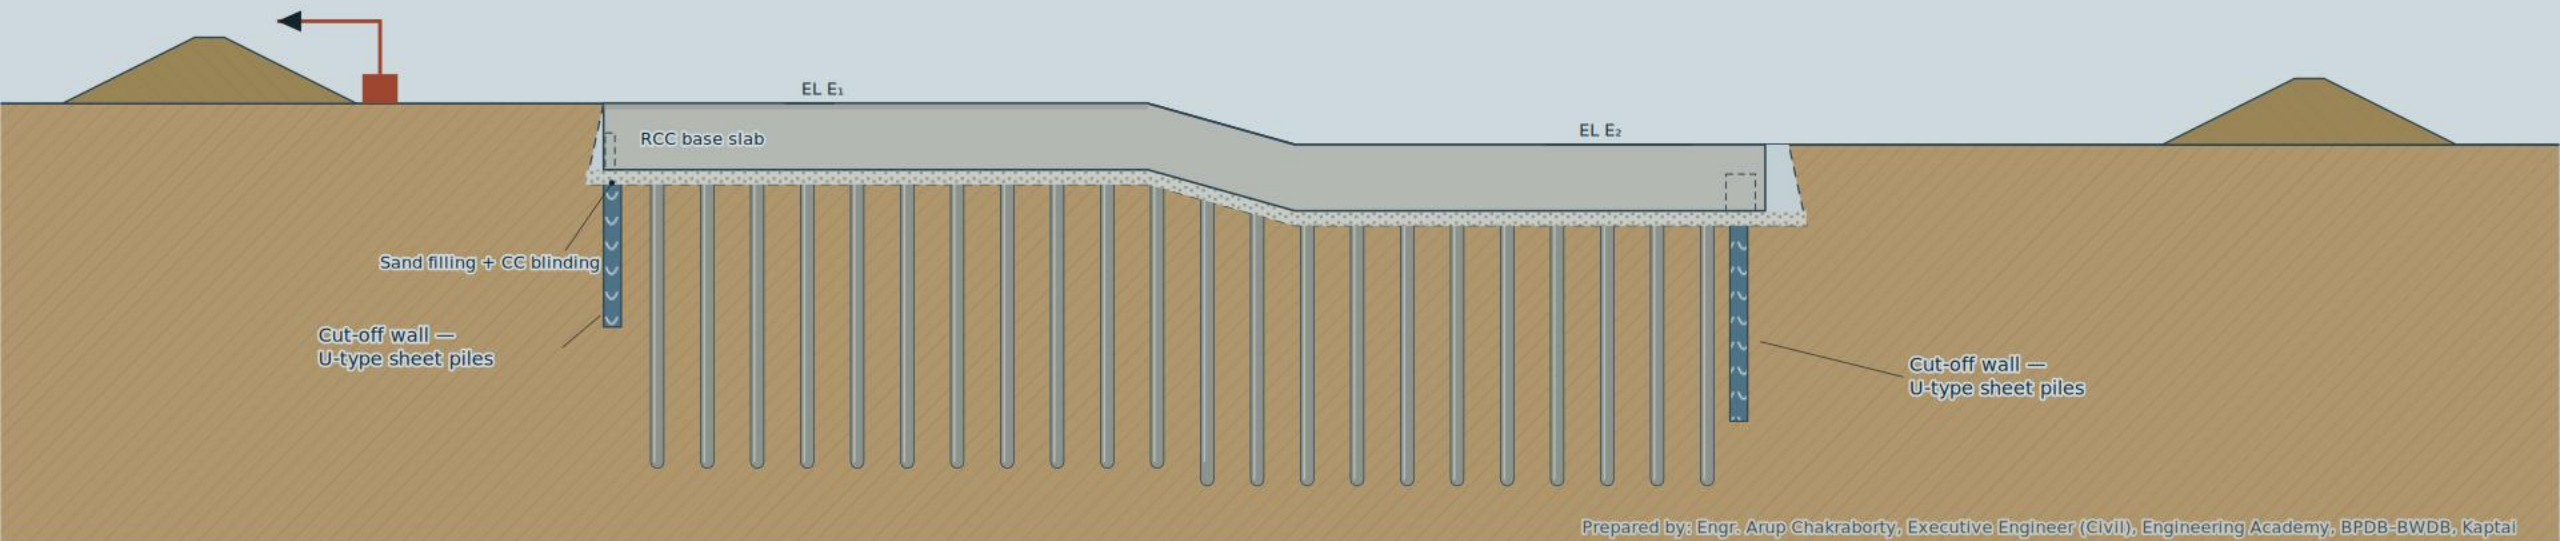



Prepared by: Engr. Arup Chakraborty, Executive Engineer (Civil), Engineering Academy, BPDB-BWDB, Kaptai

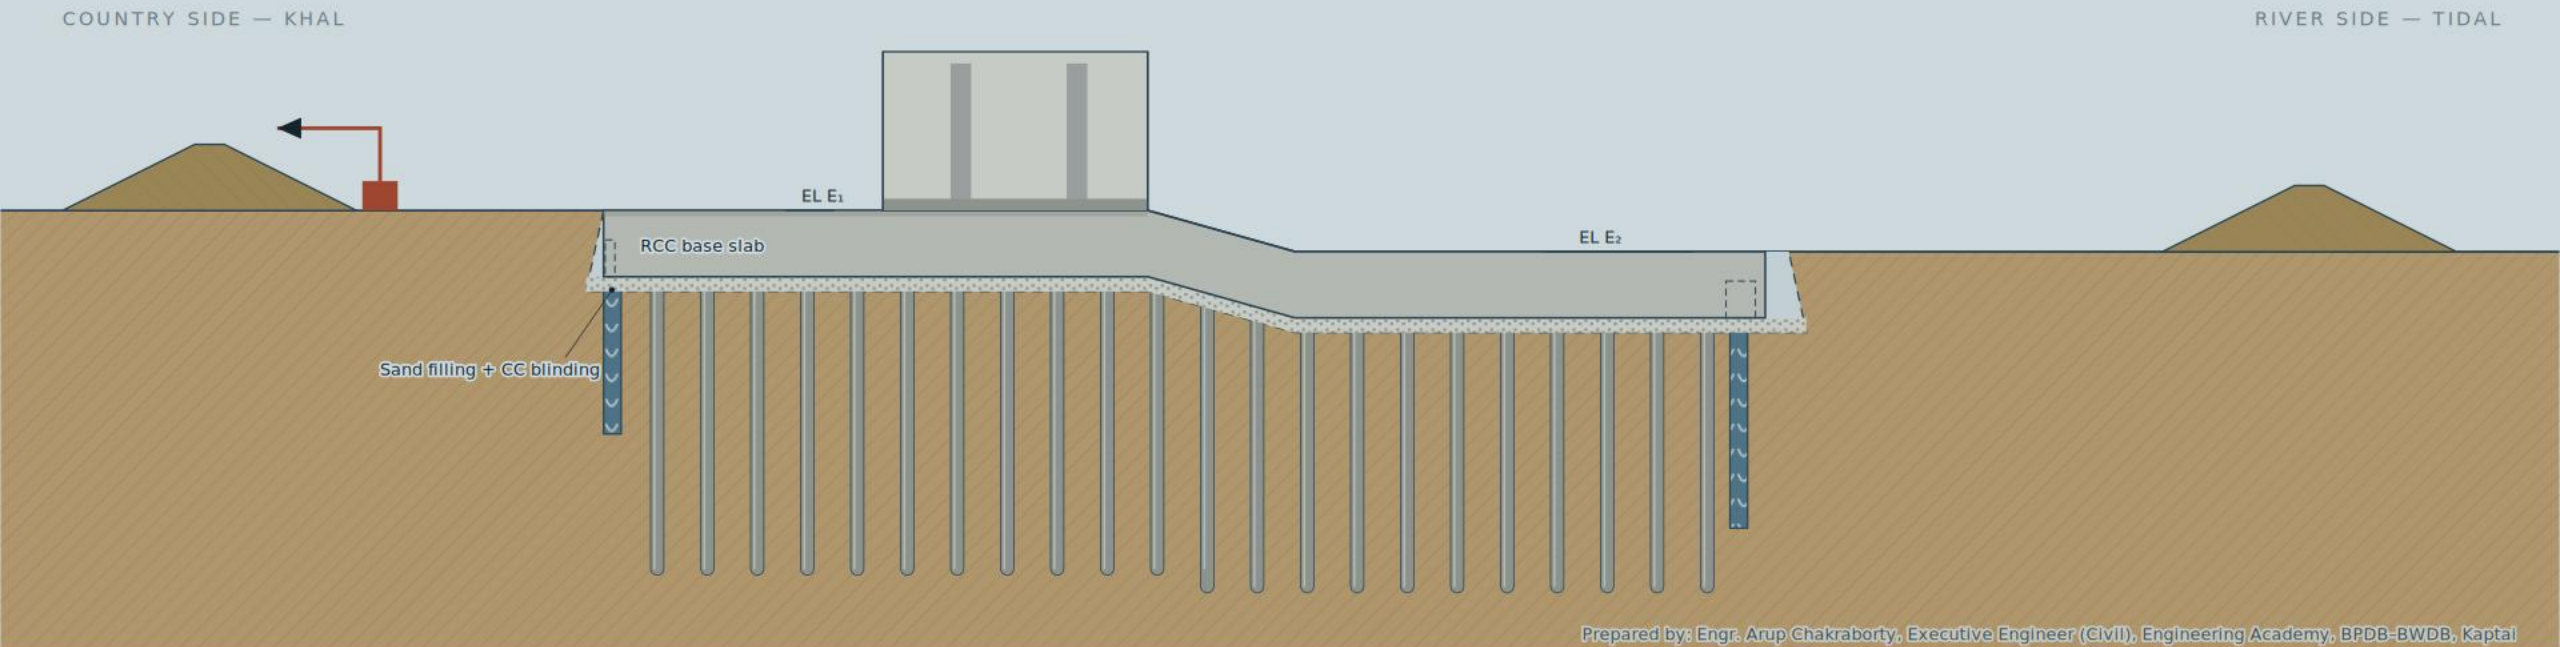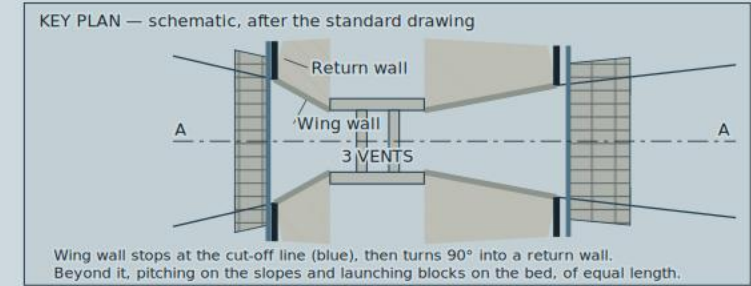


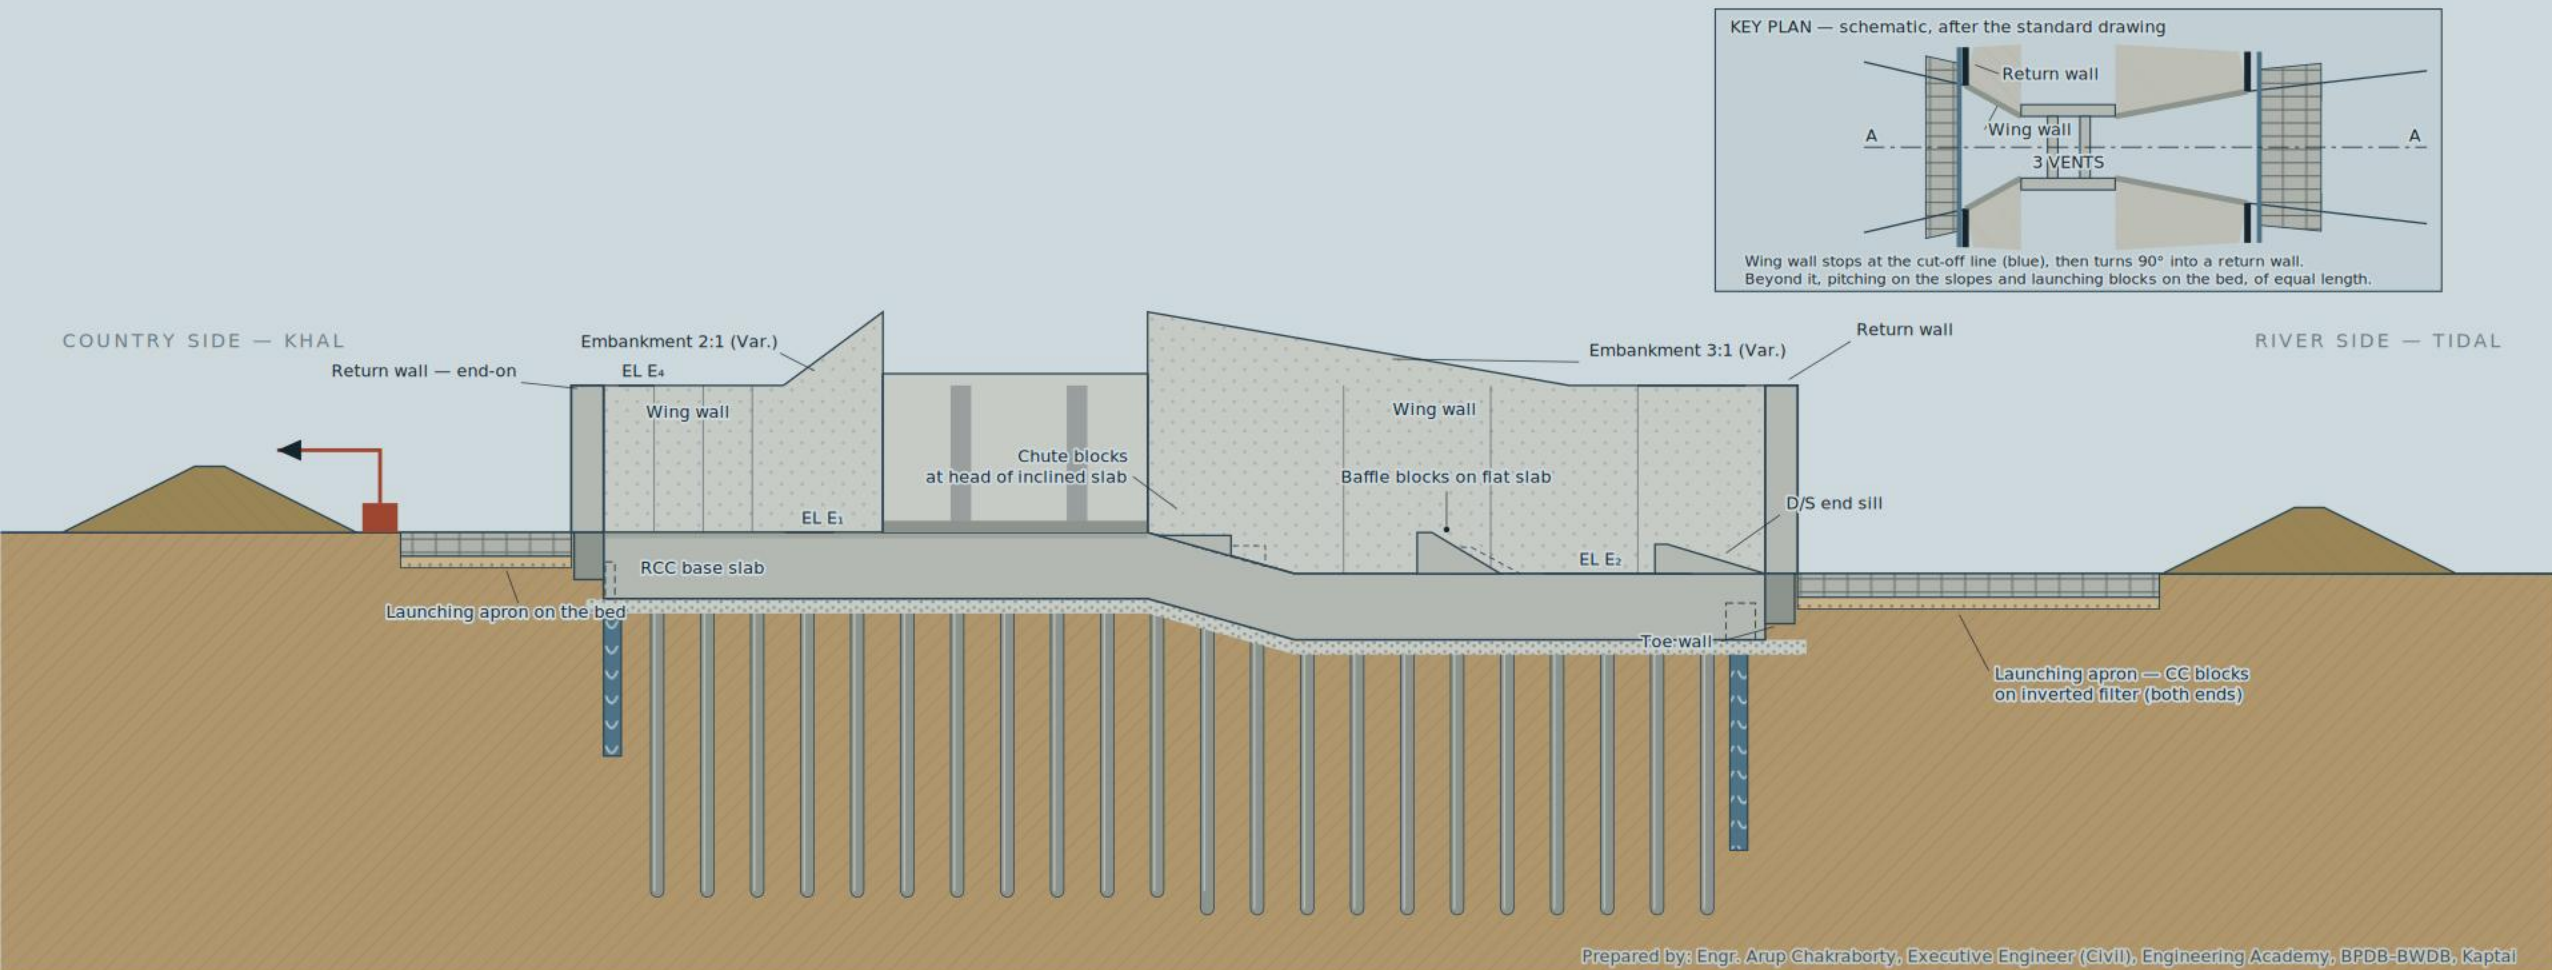


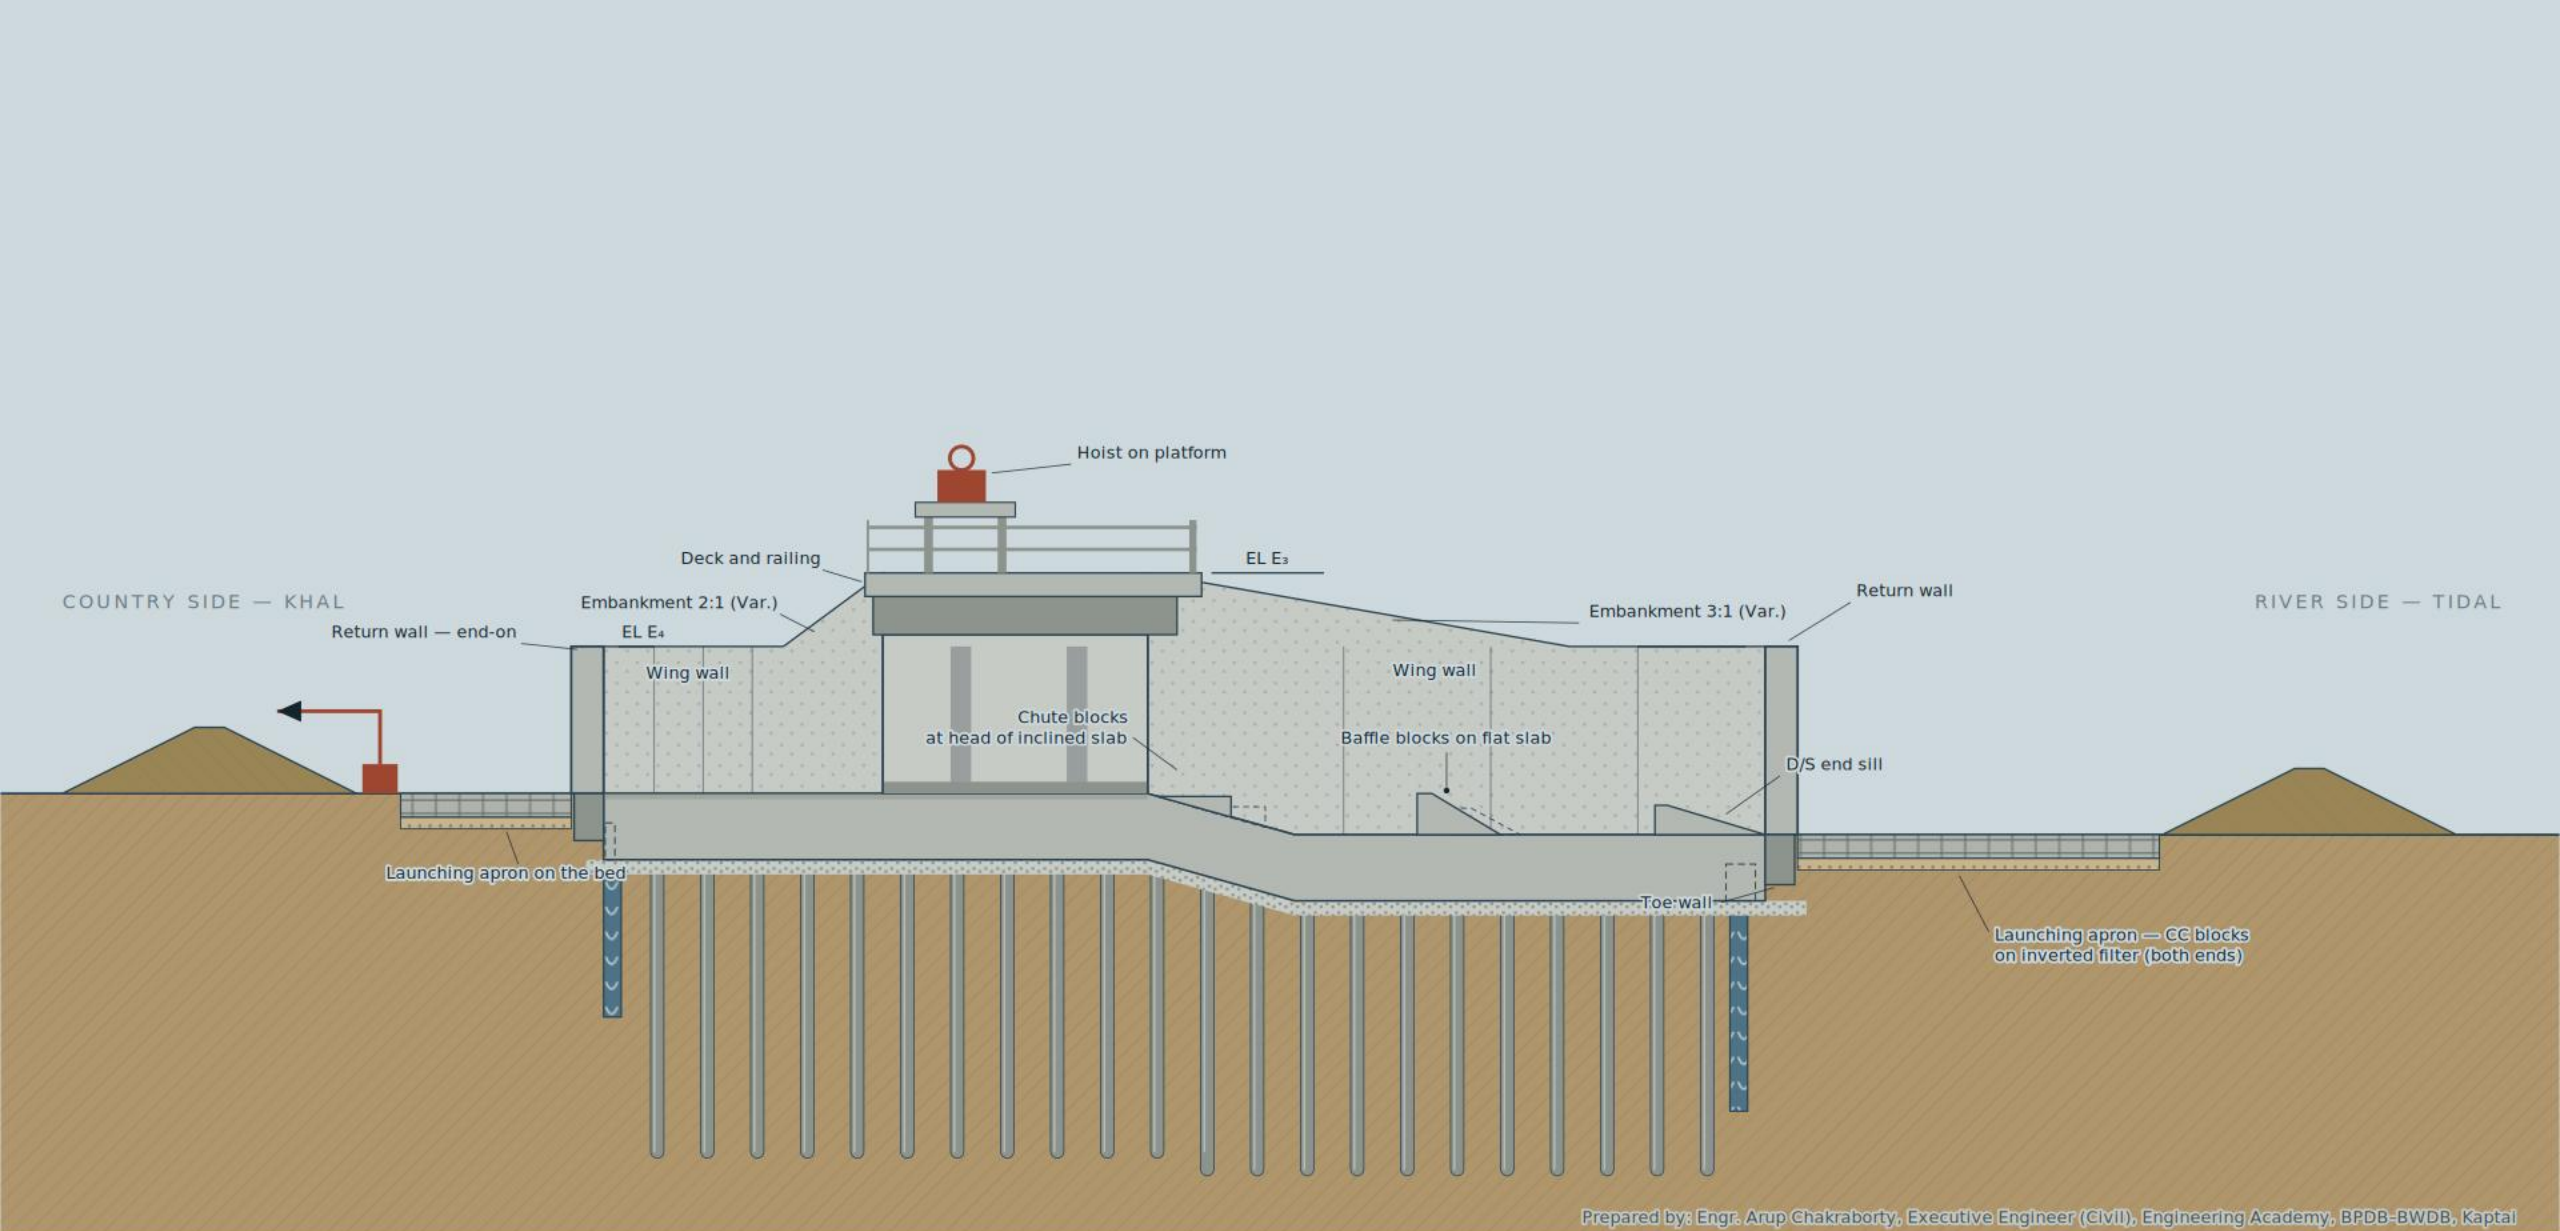


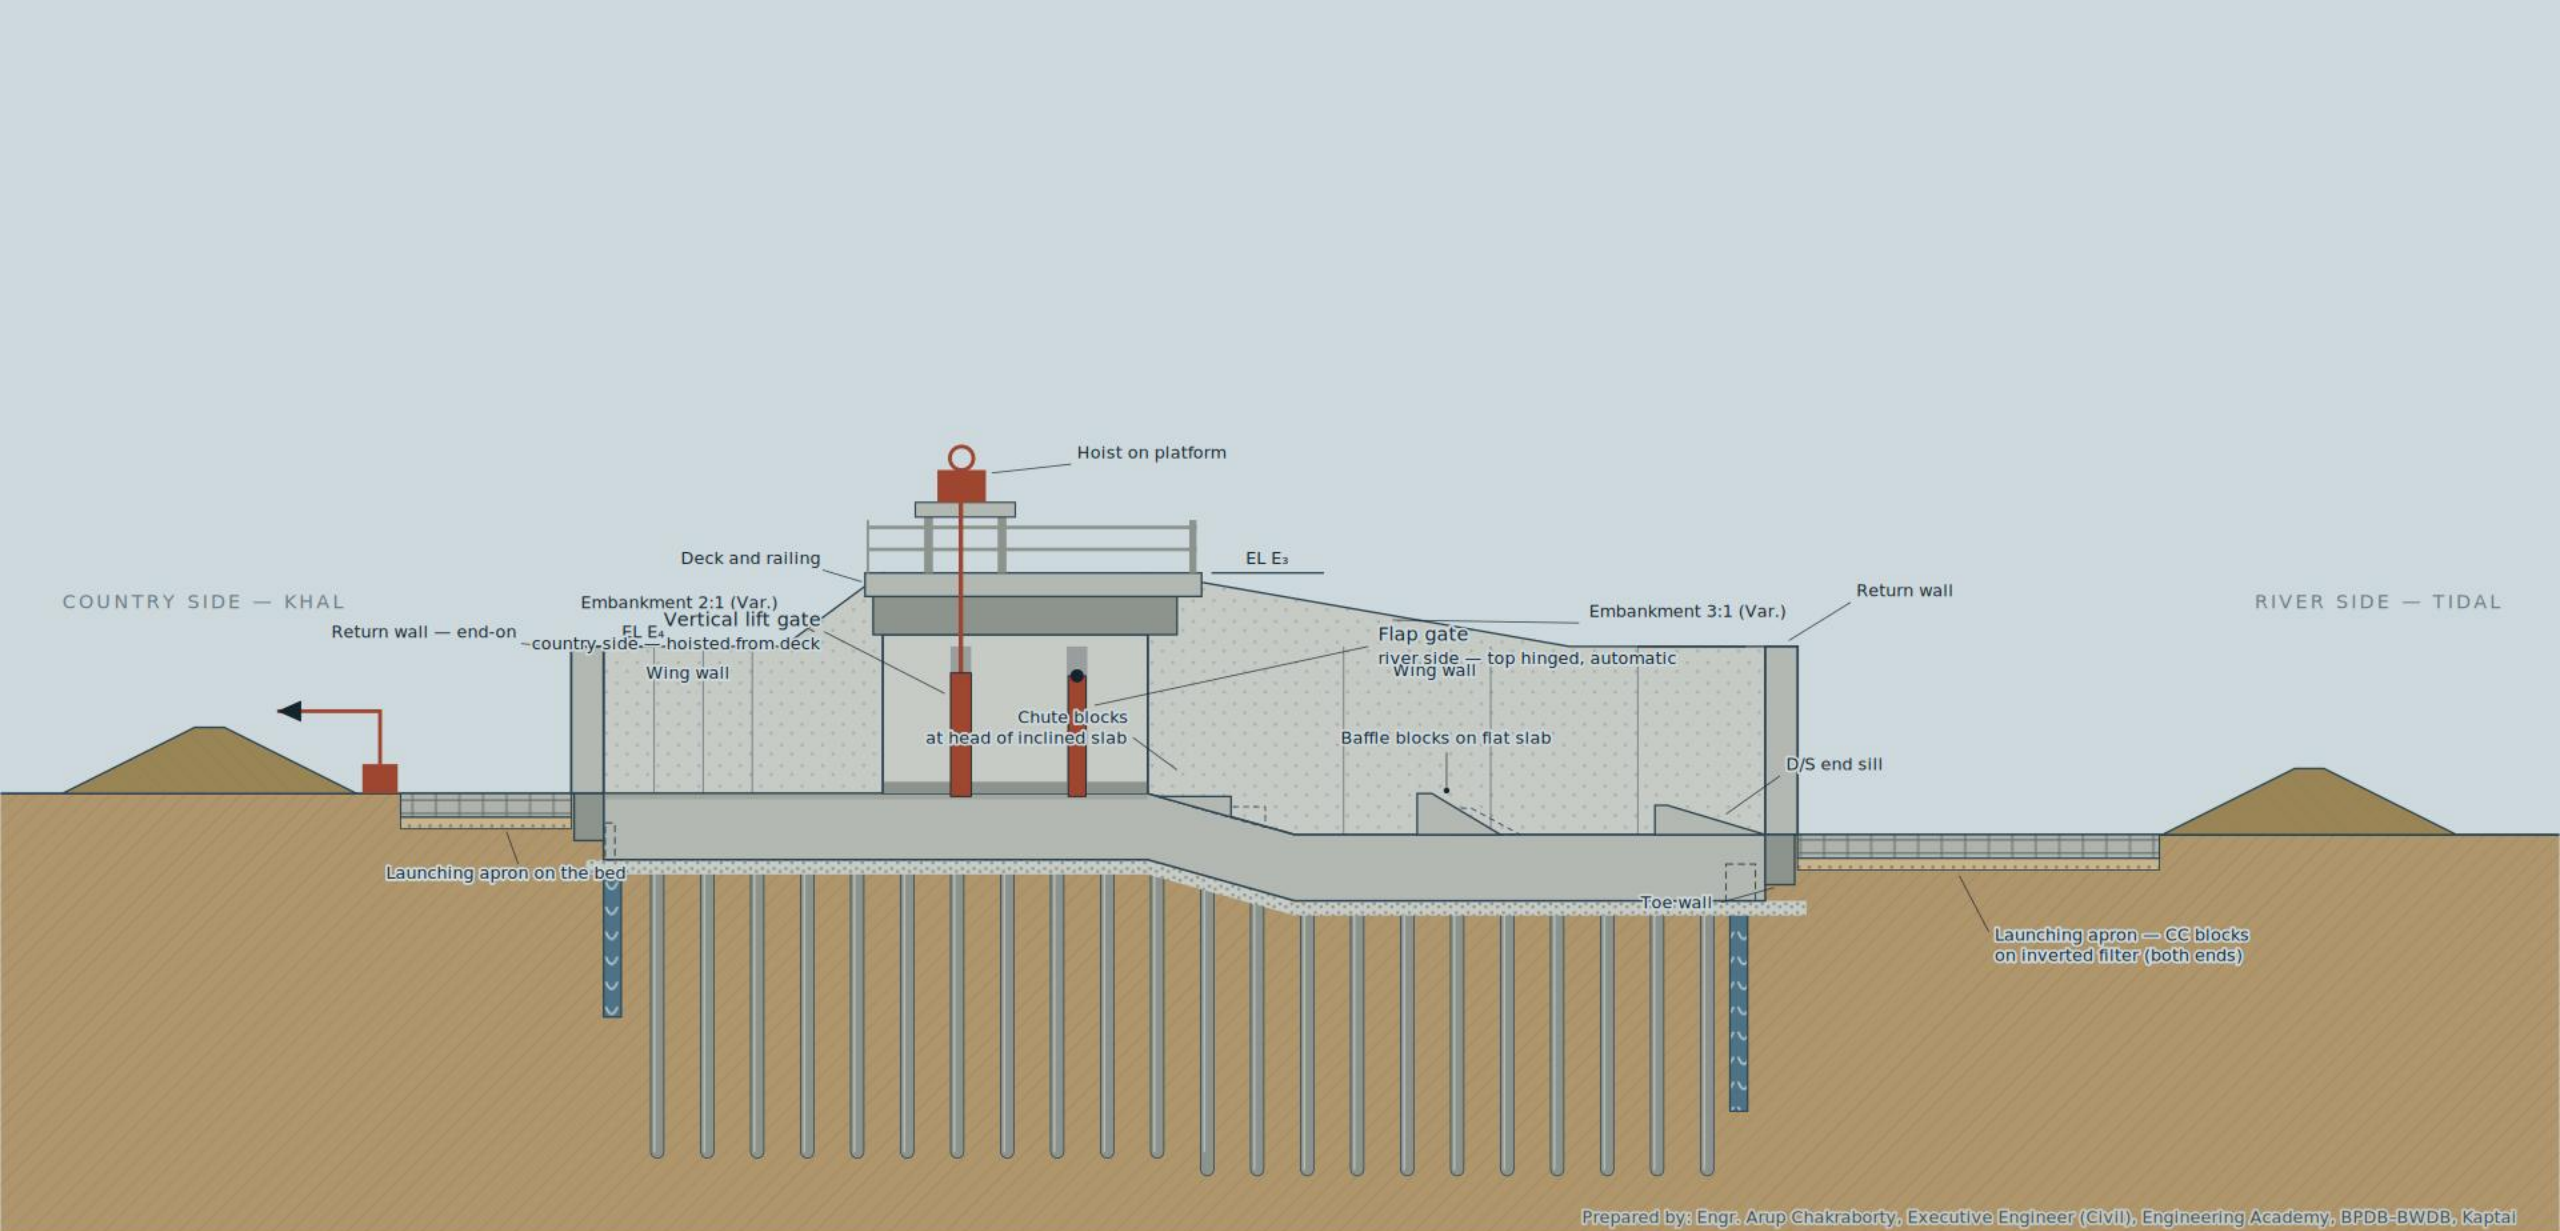

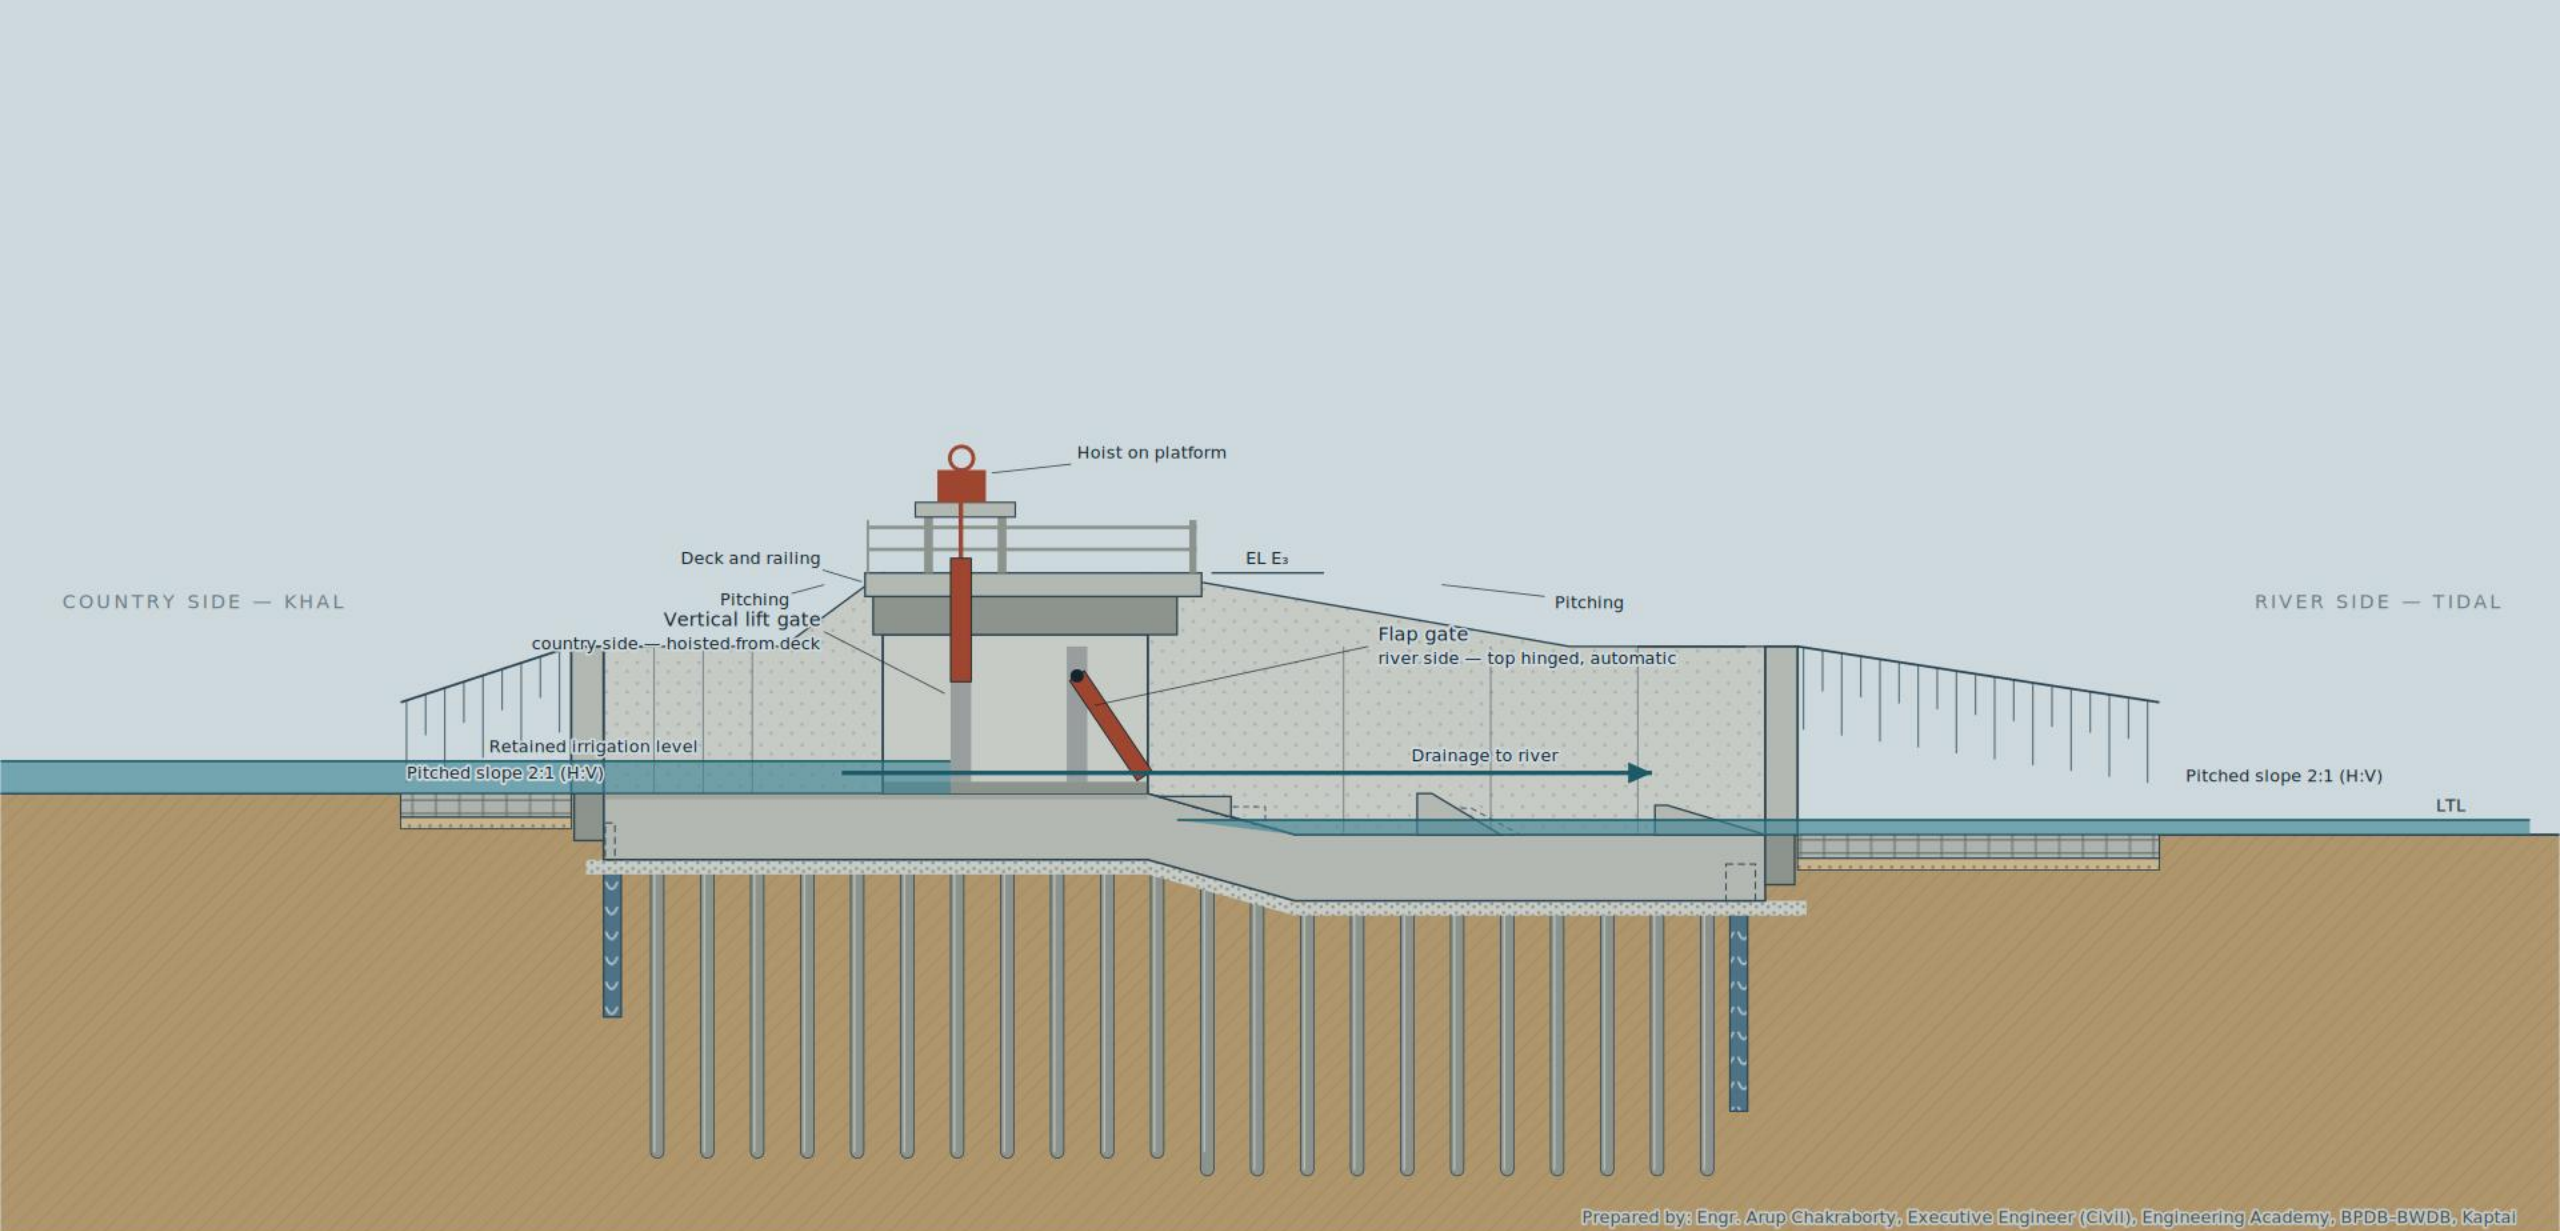

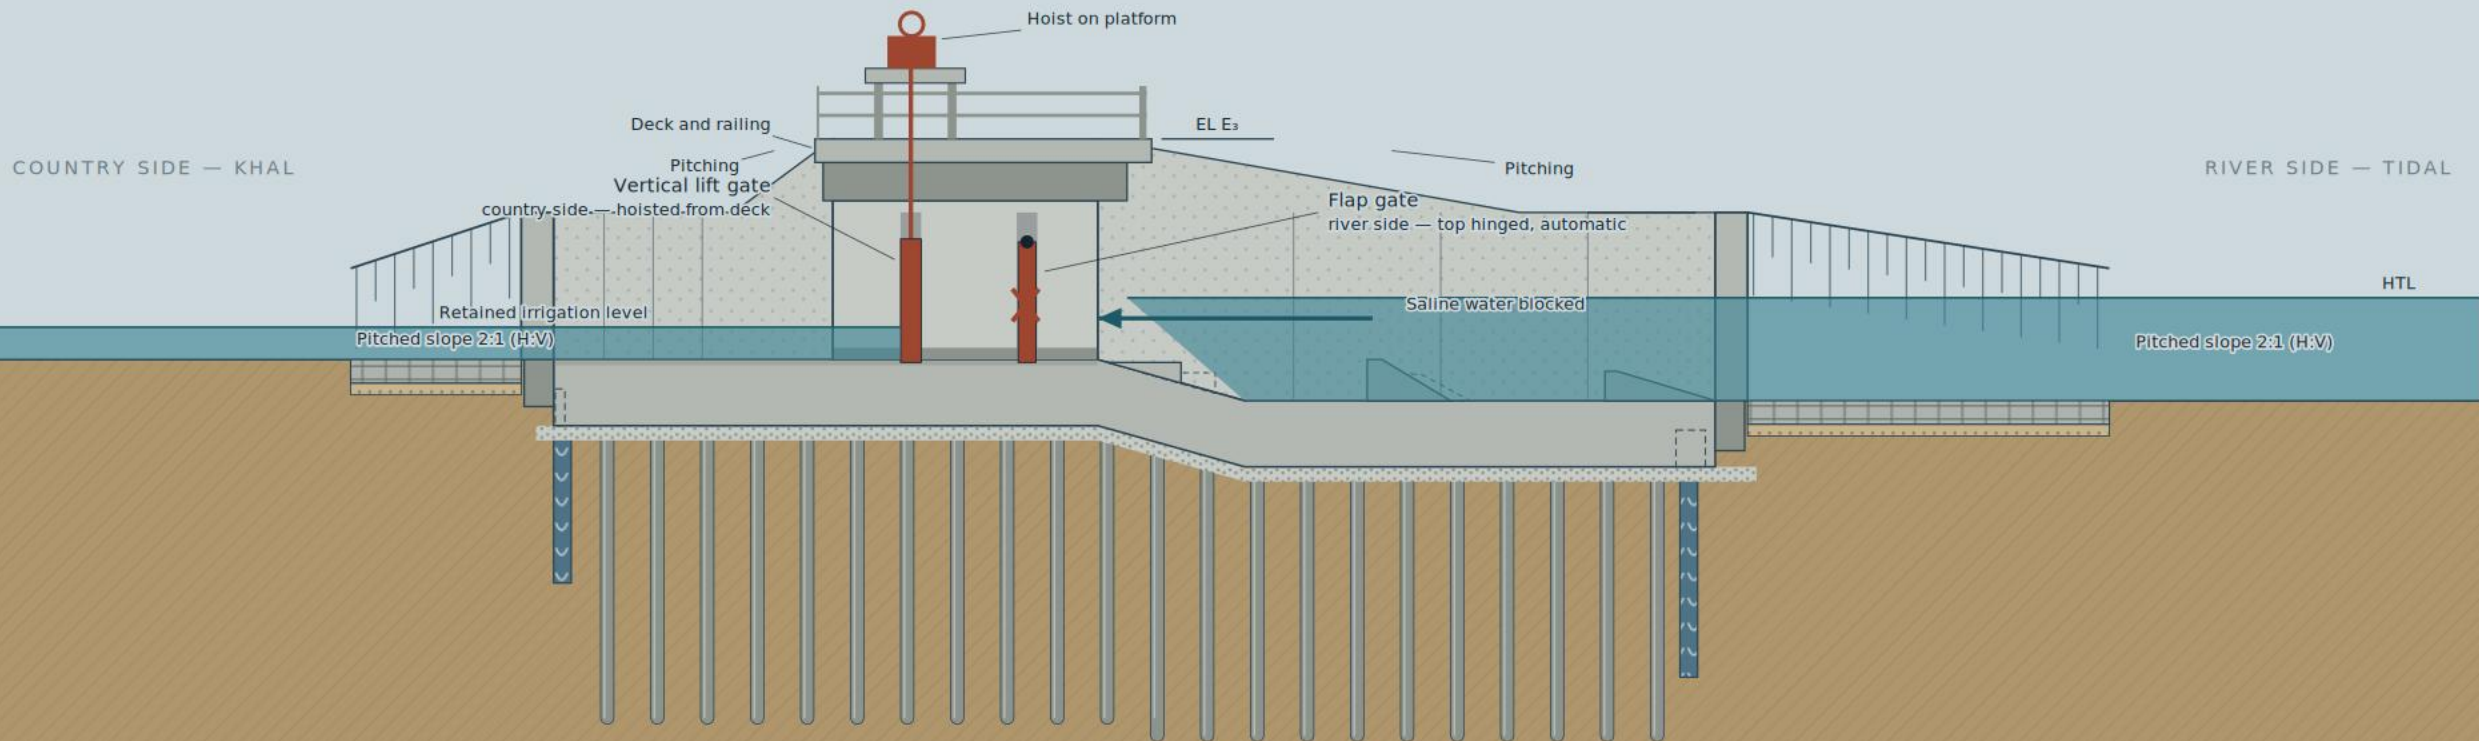

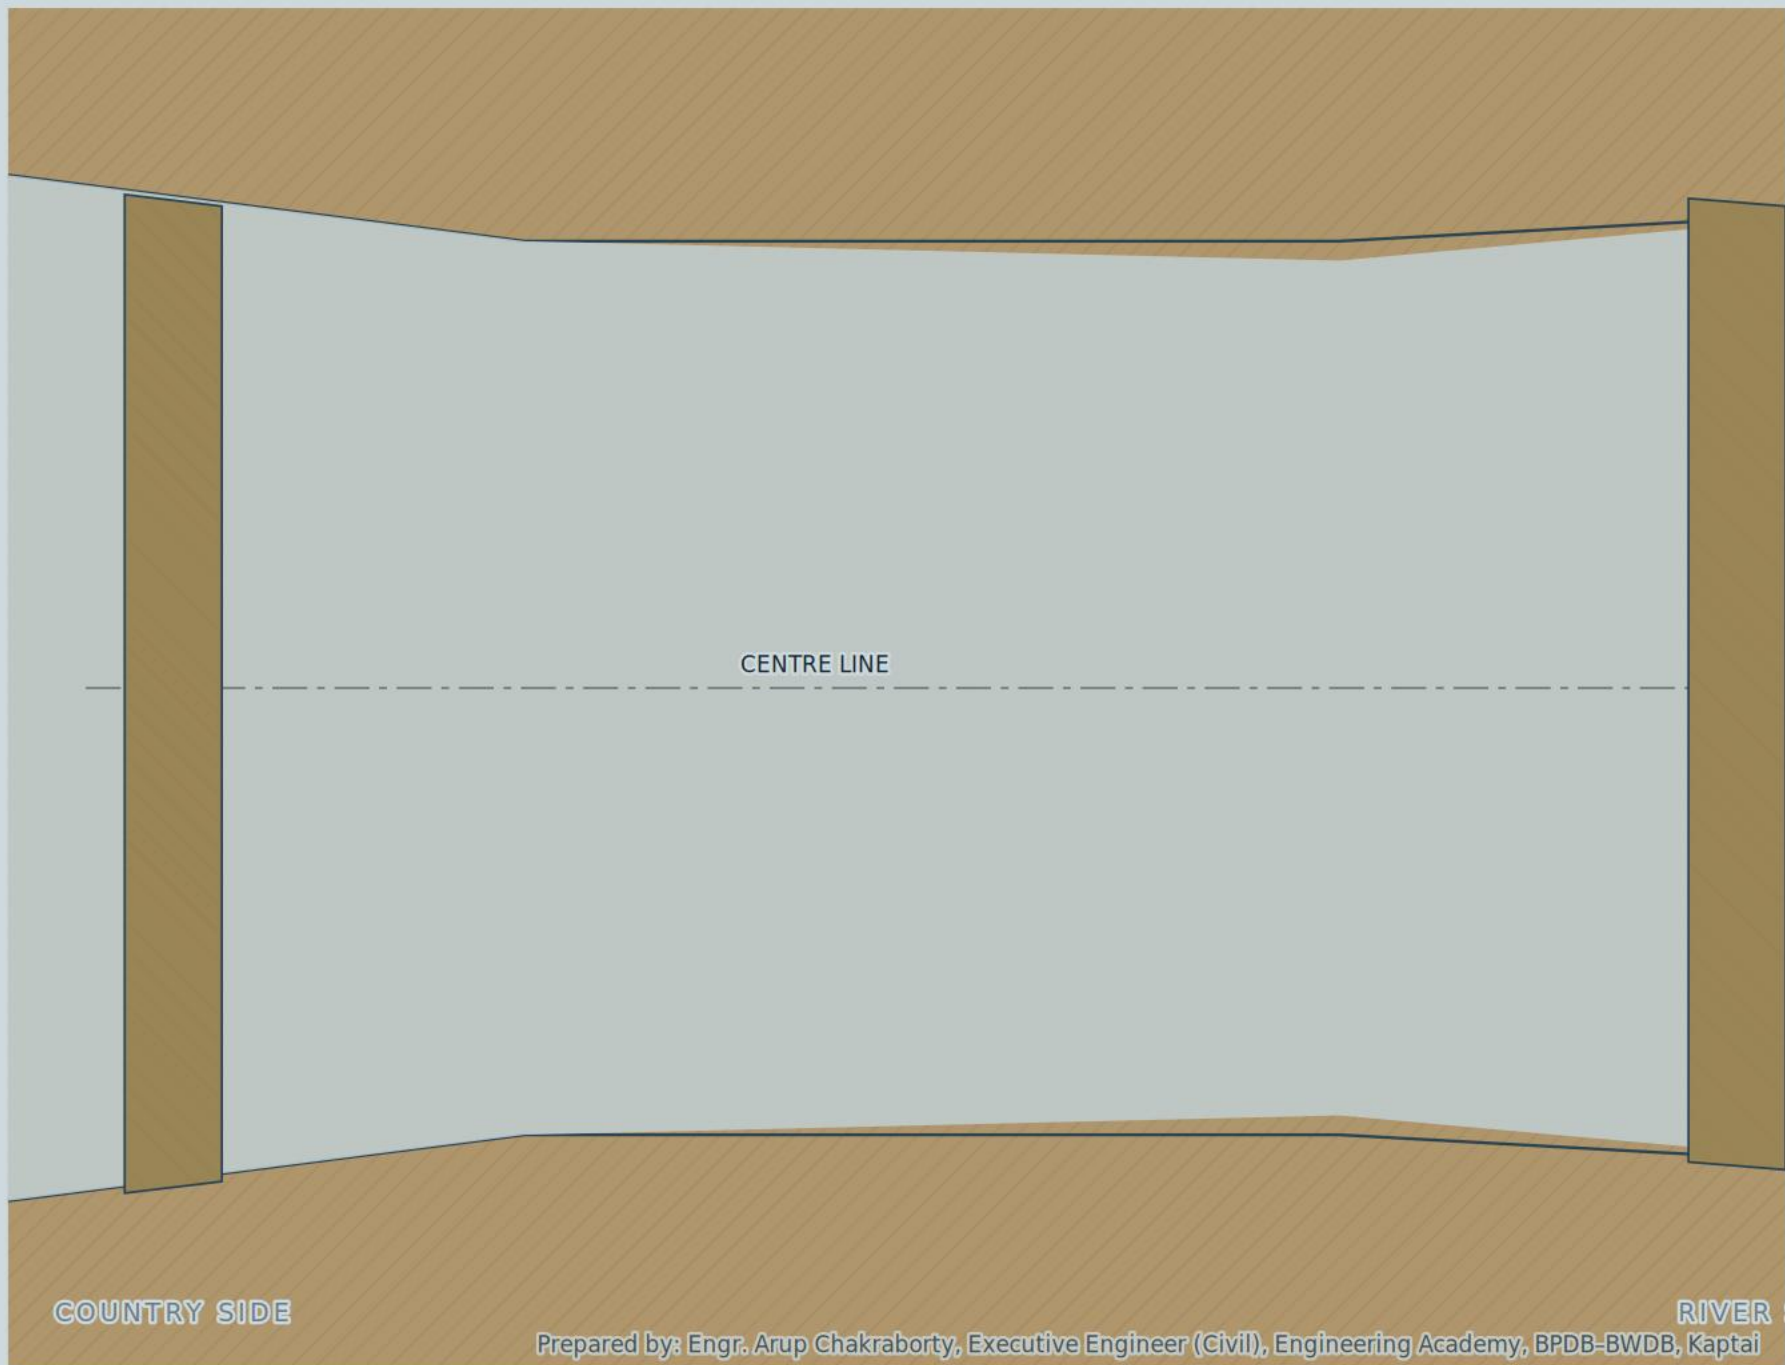


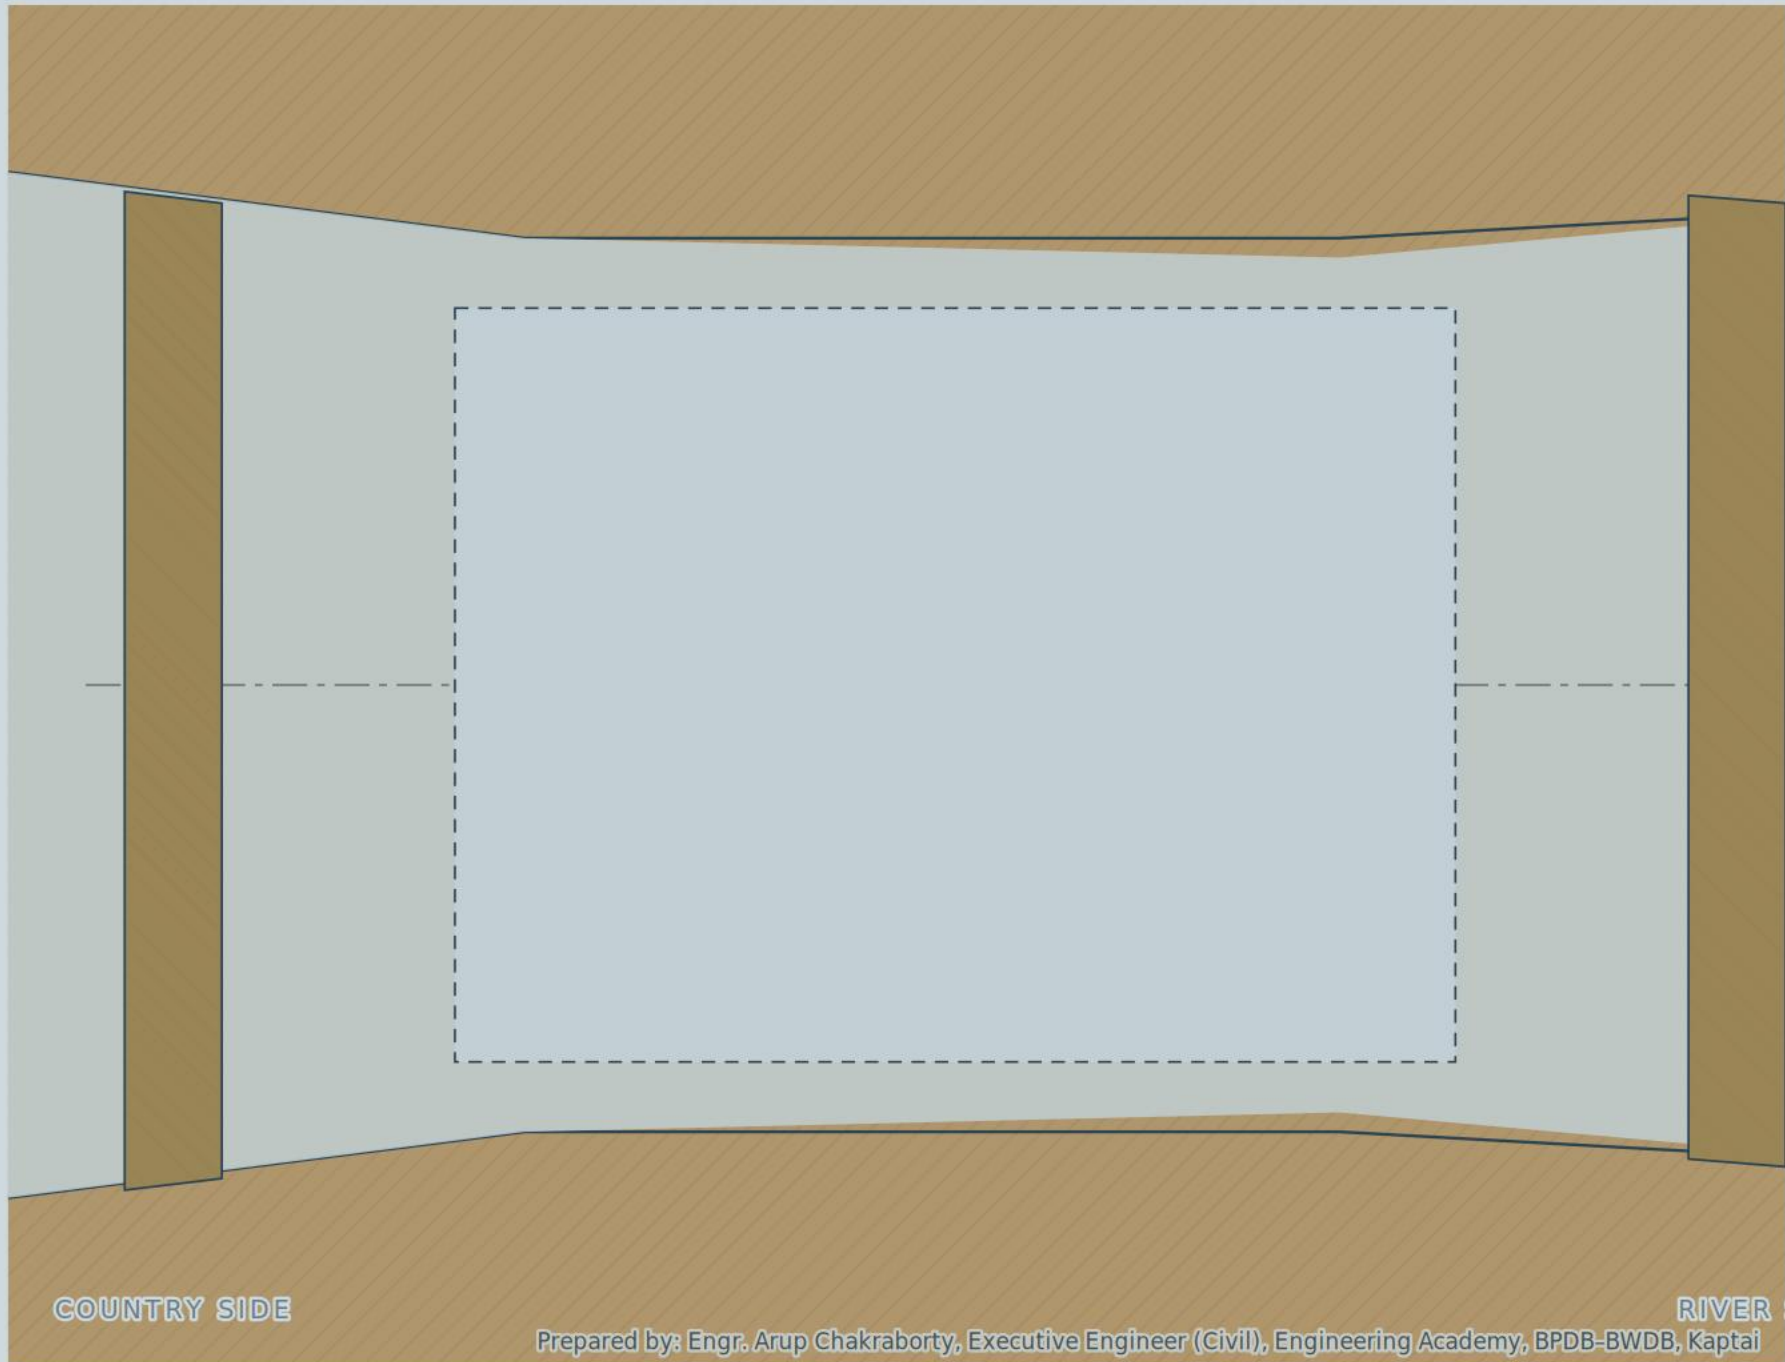



COUNTRY SIDE


RIVER


Prepared by: Engr. Arup Chakraborty, Executive Engineer (Civil), Engineering Academy, BPDB-BWDB, Kaptai

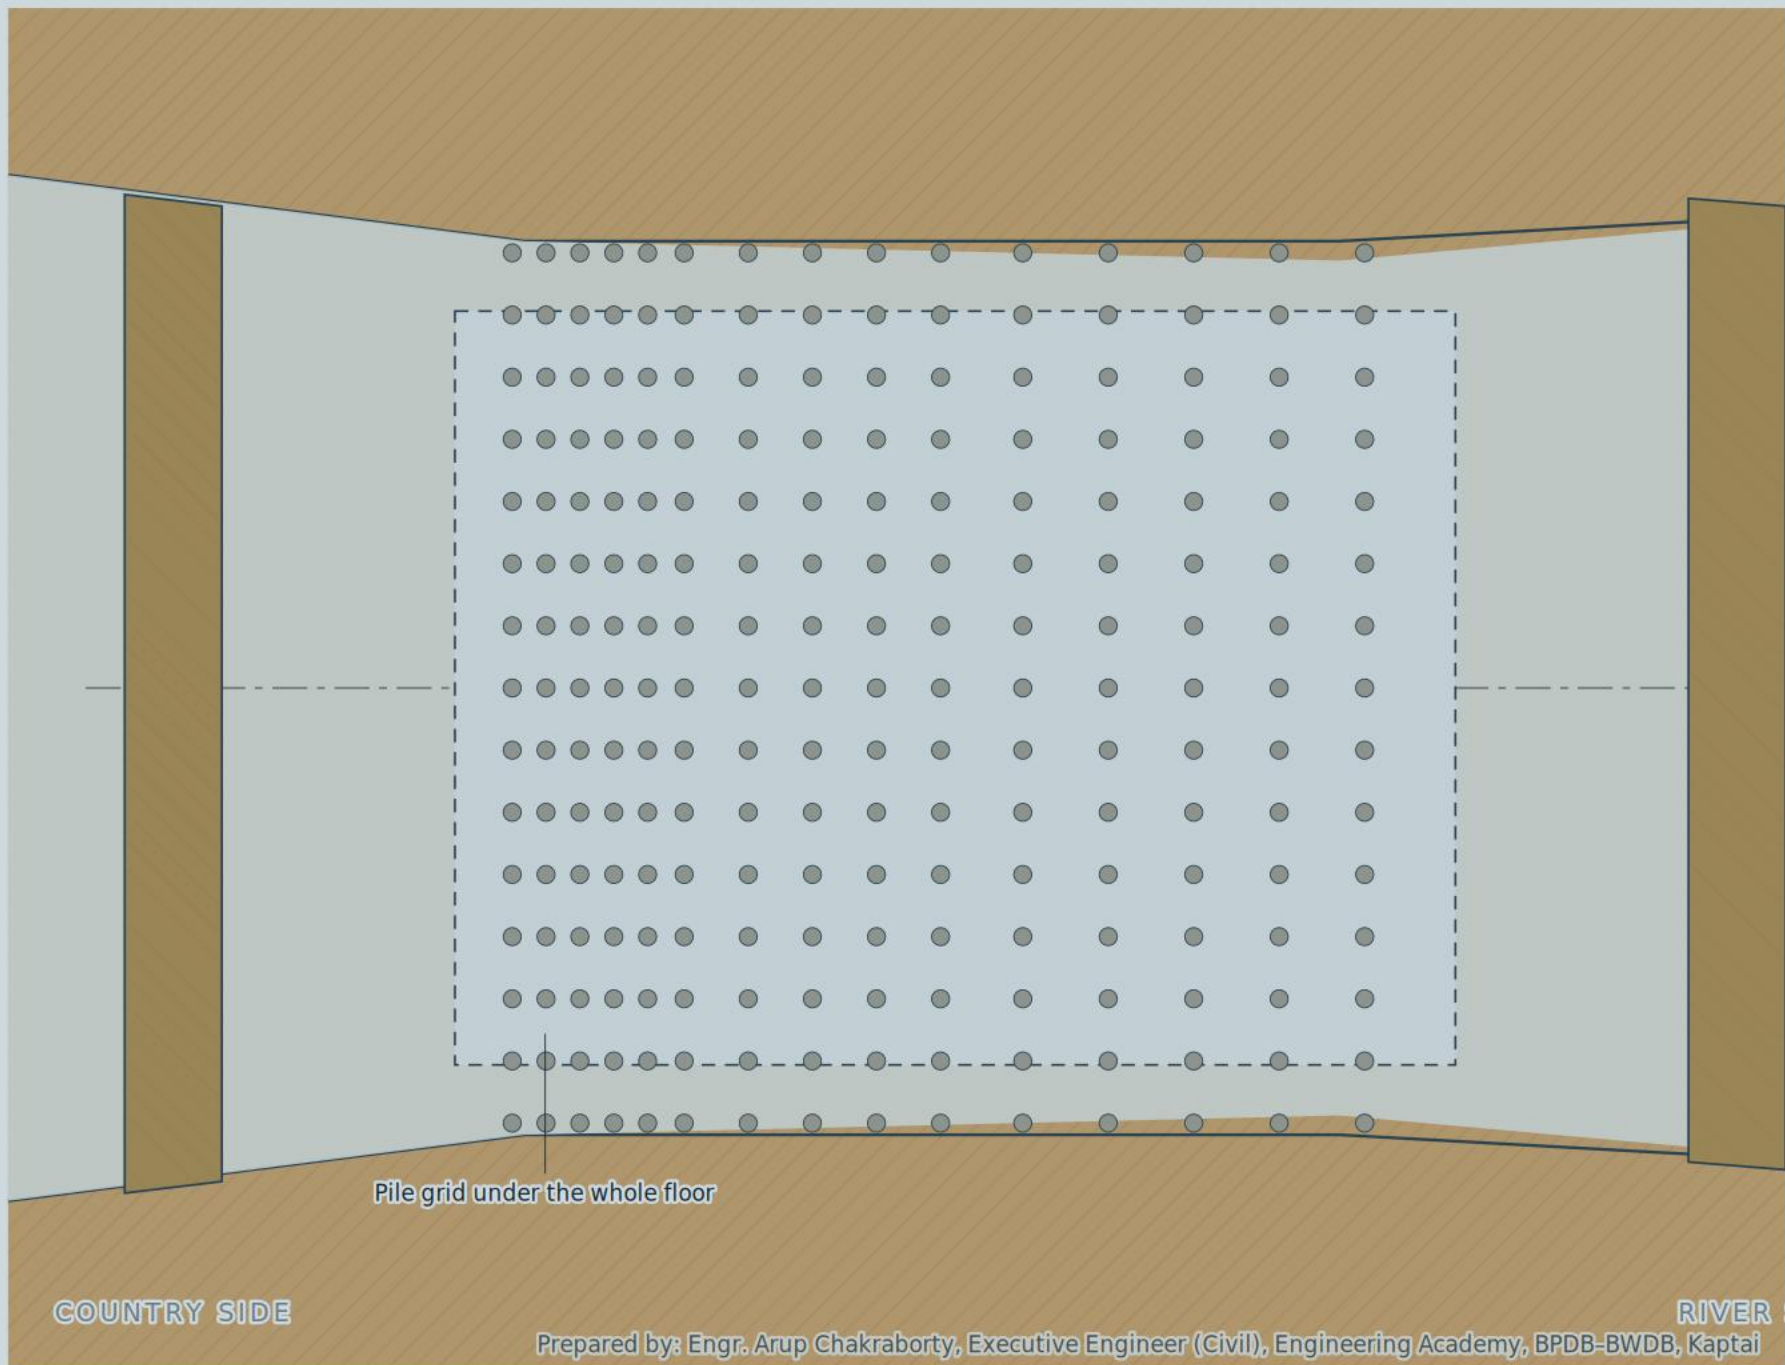


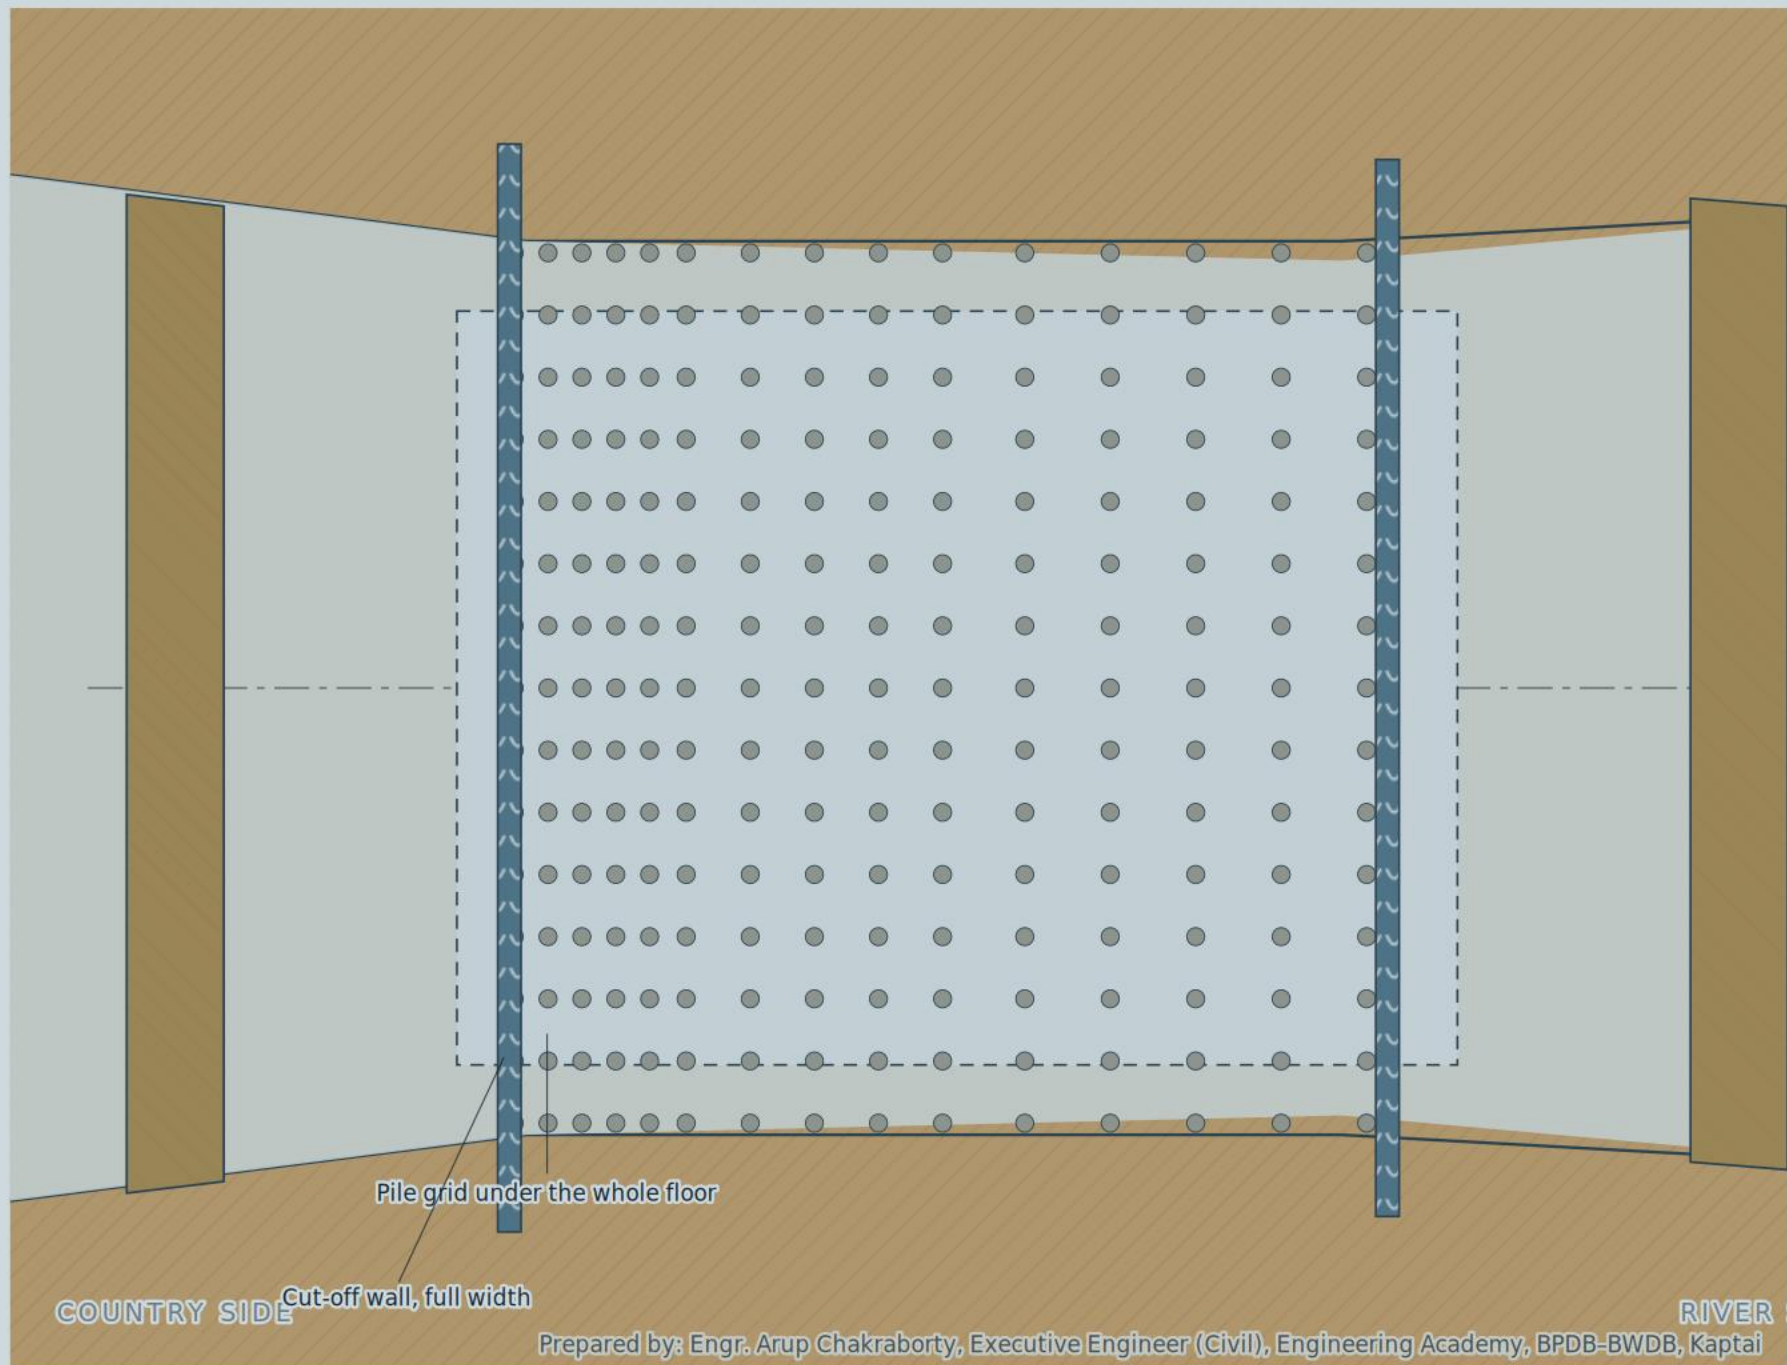


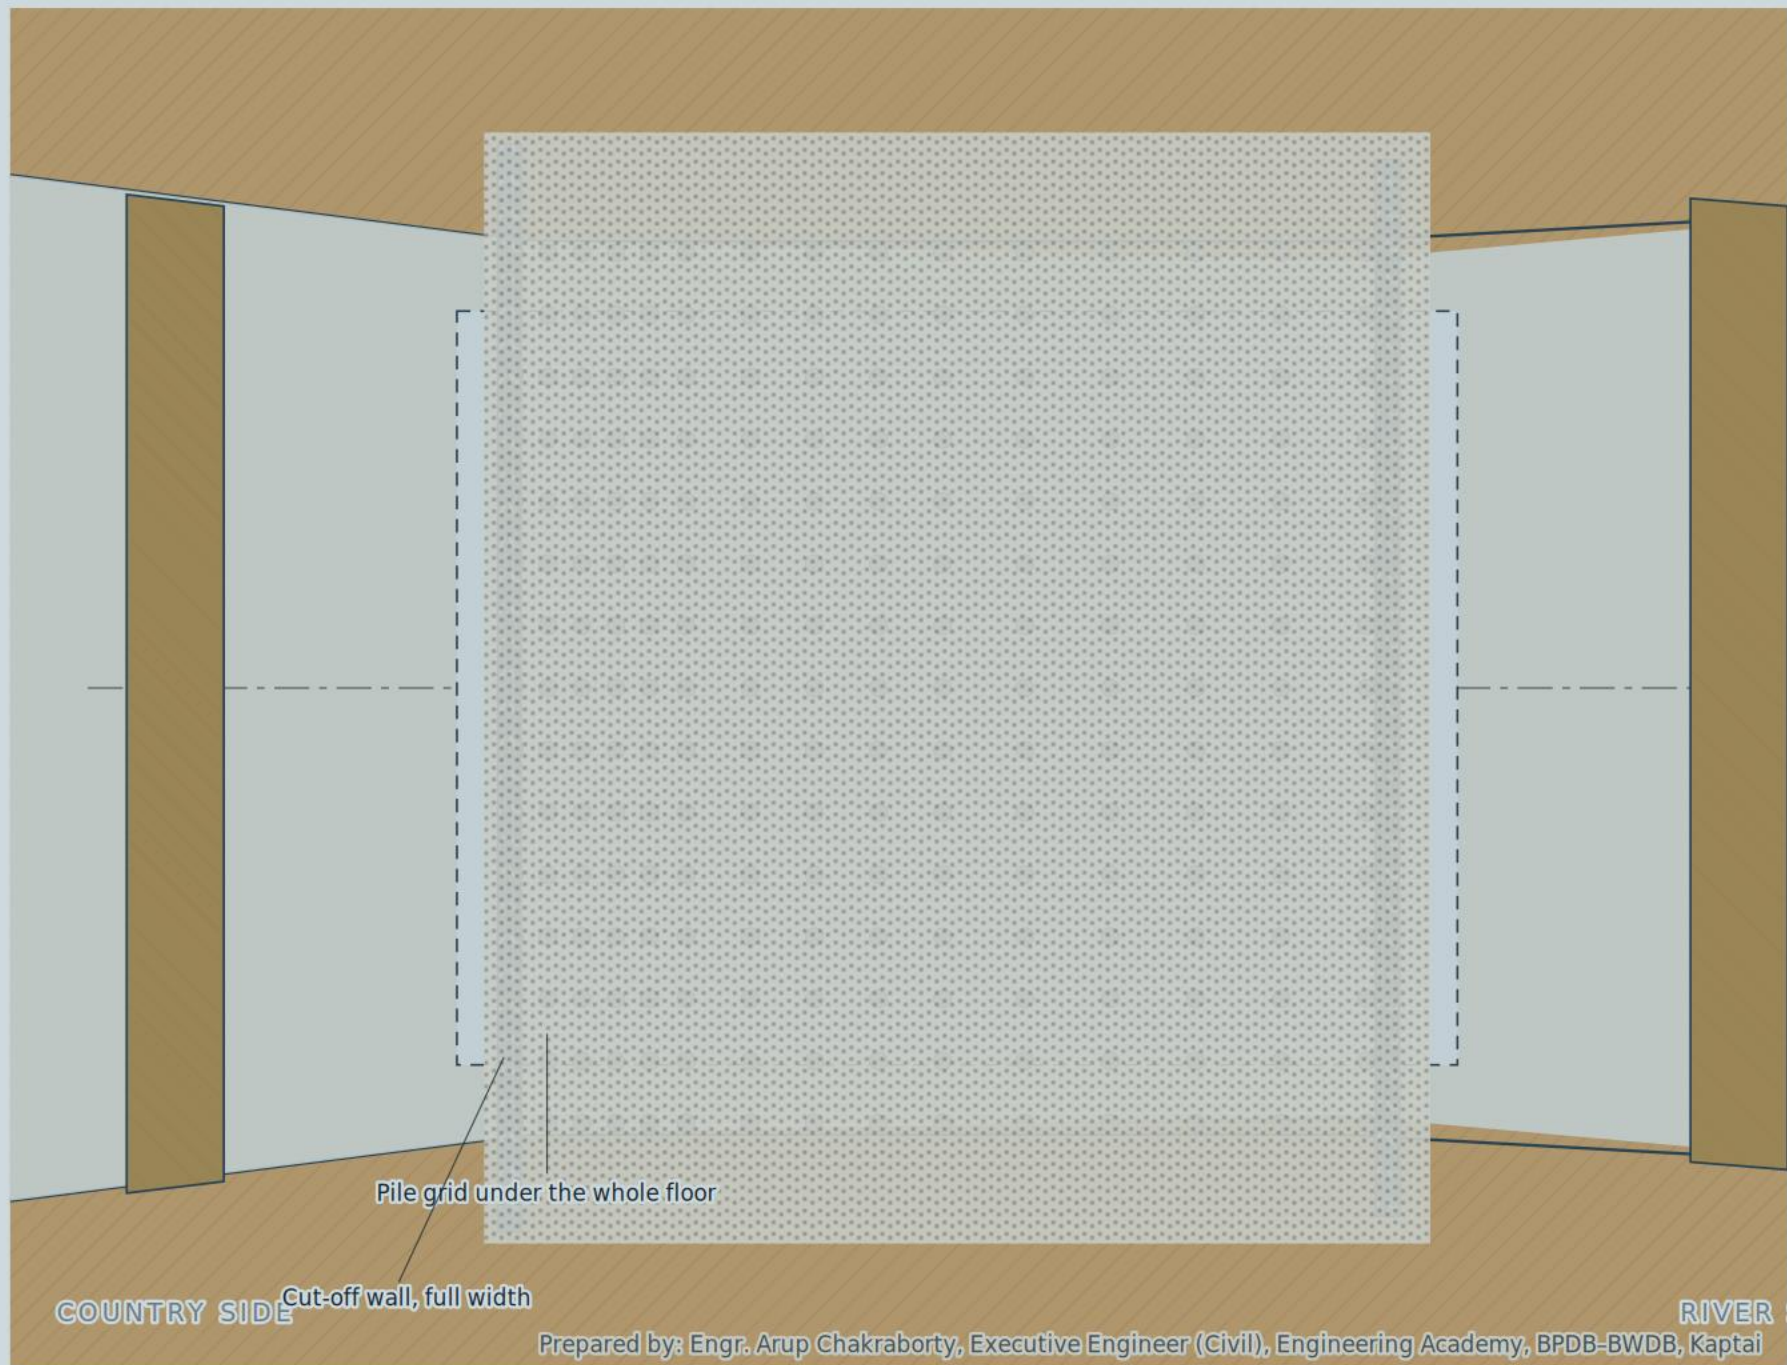


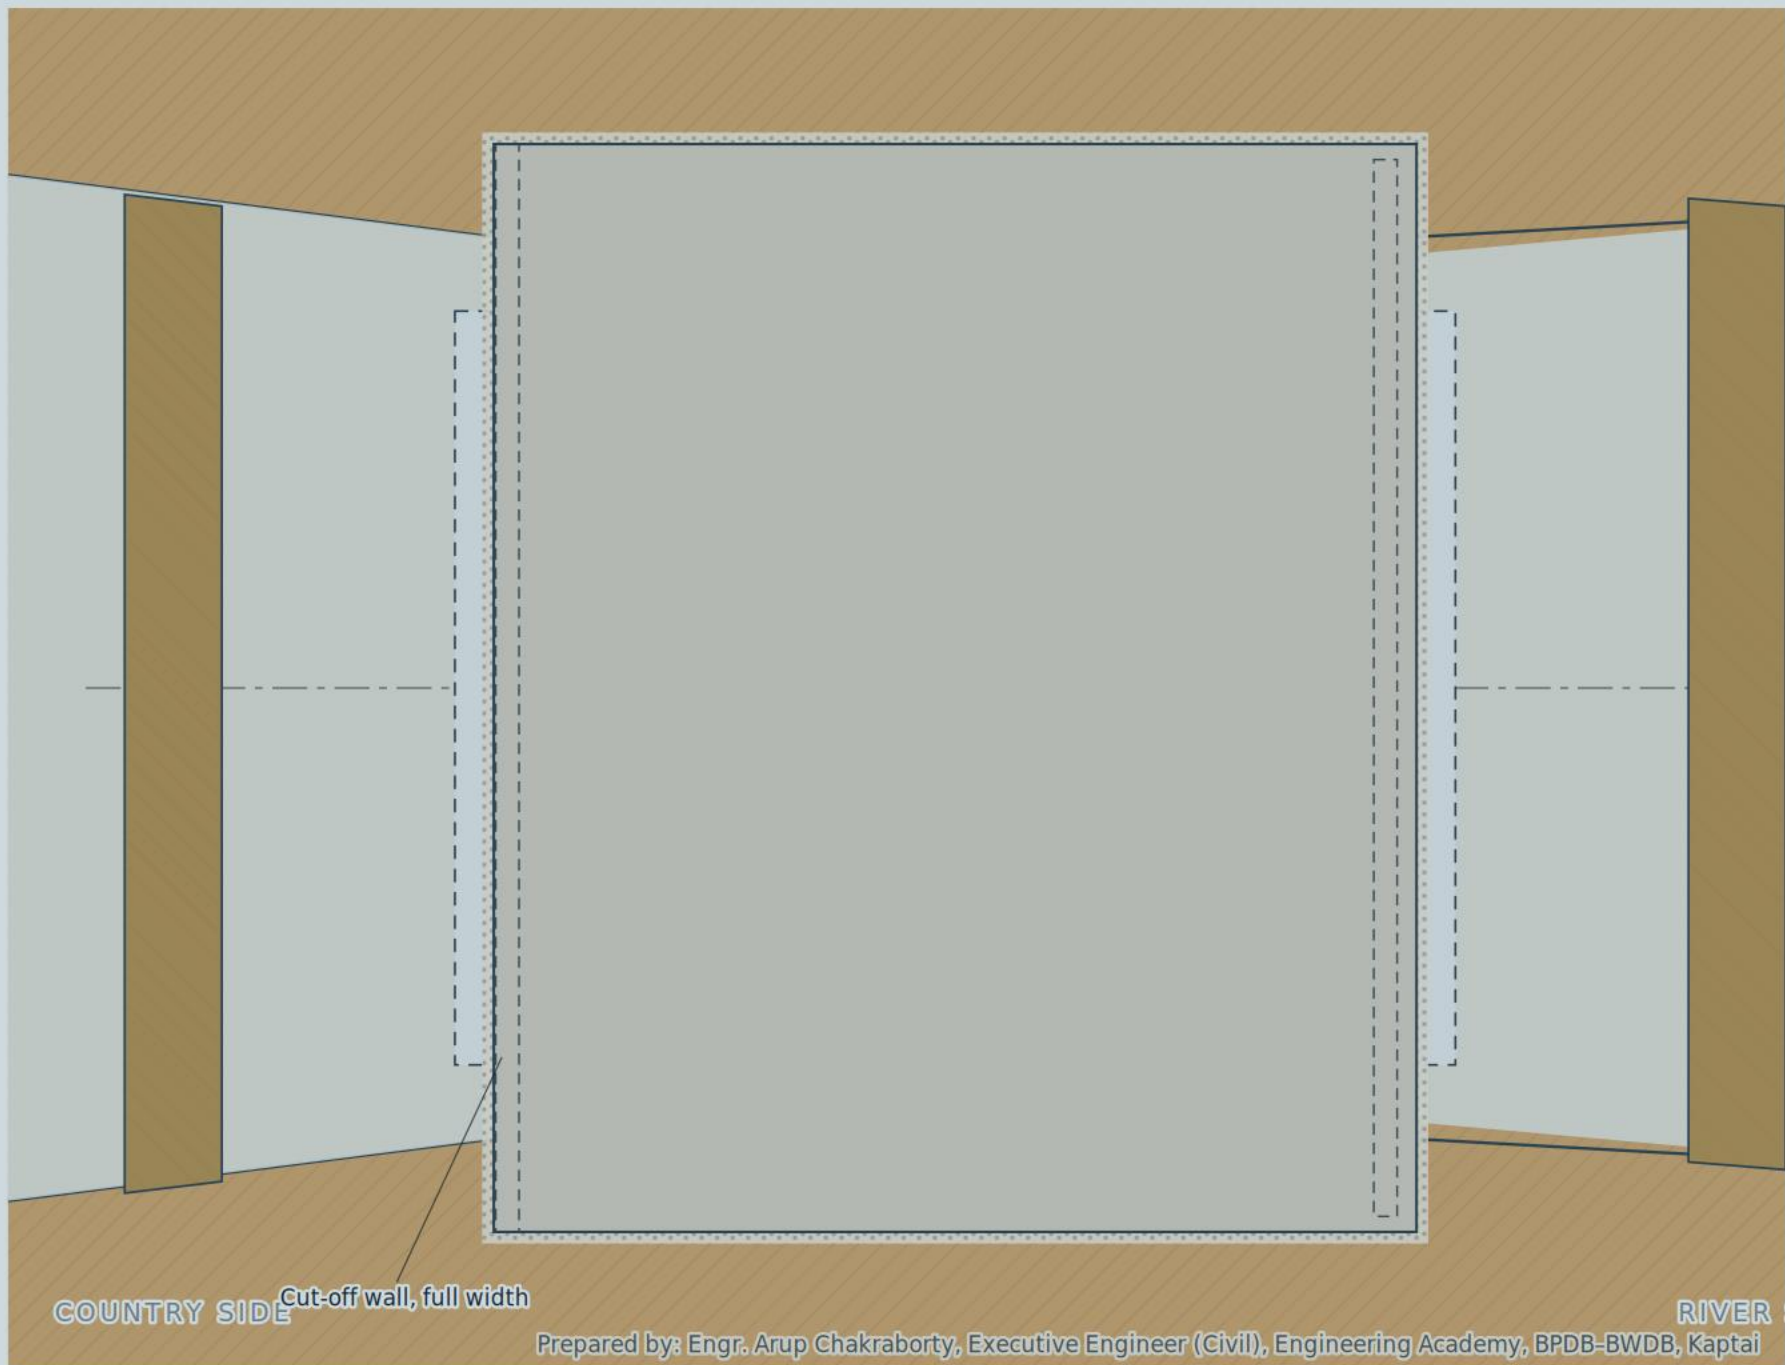


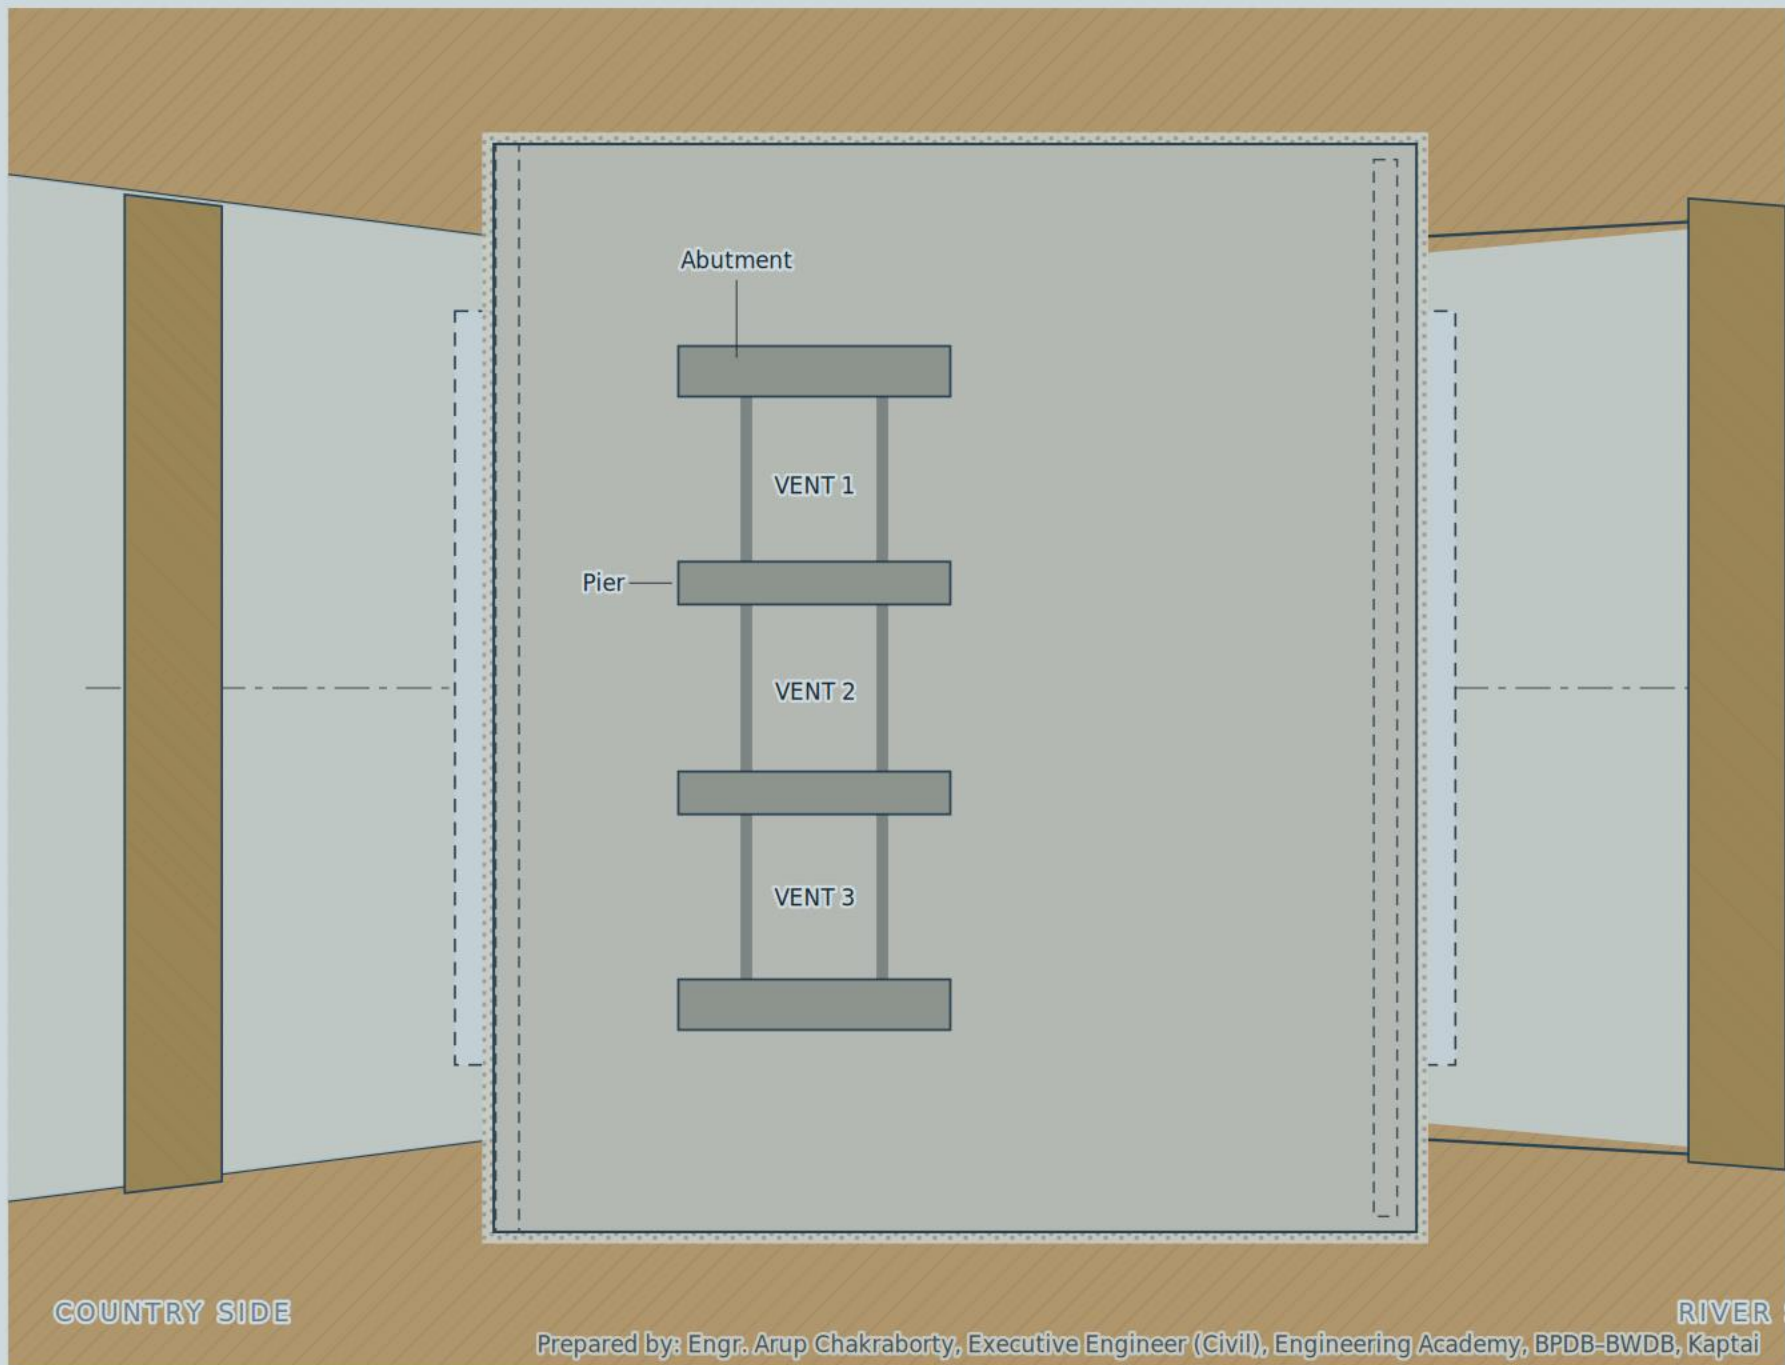


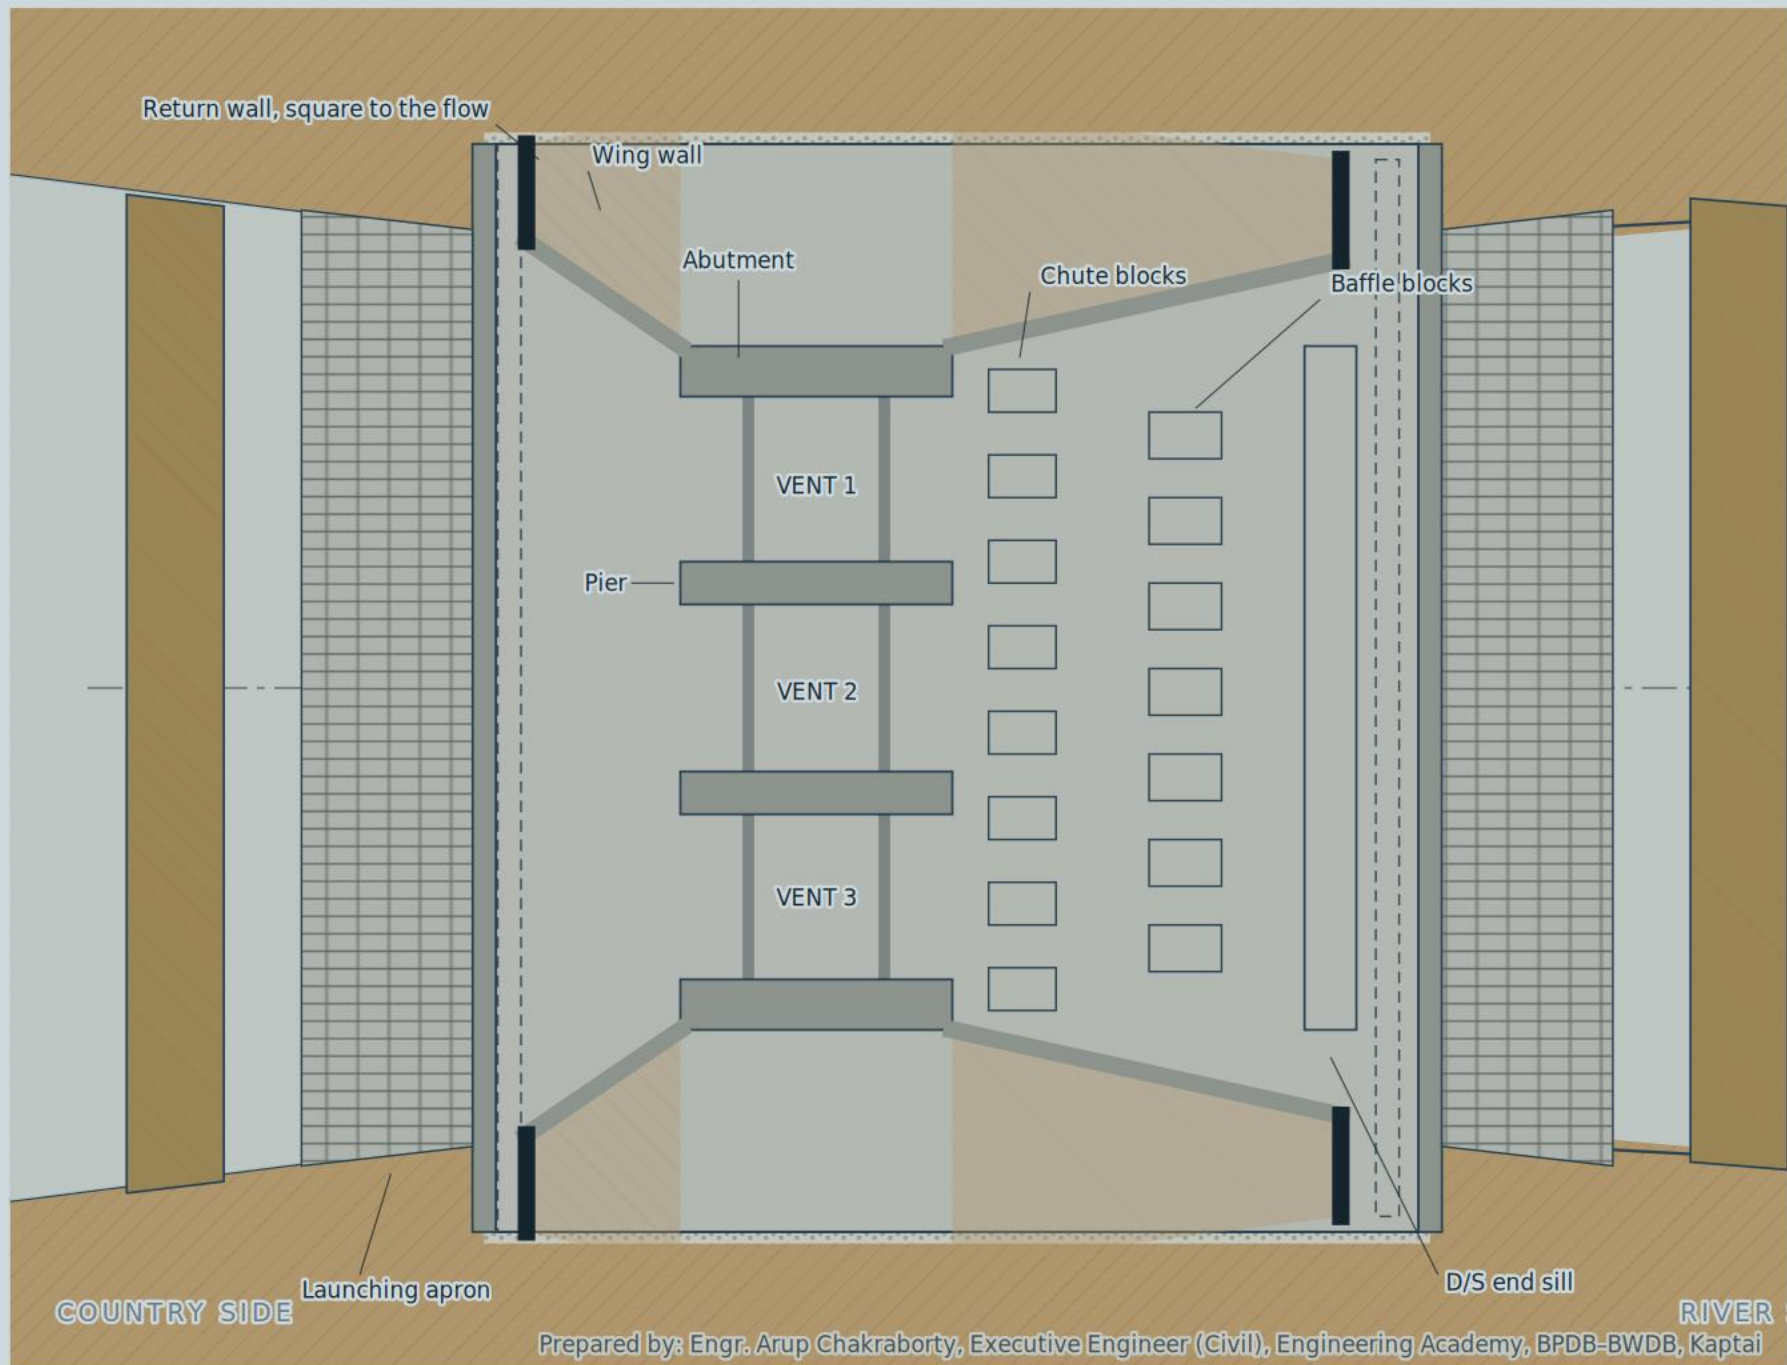

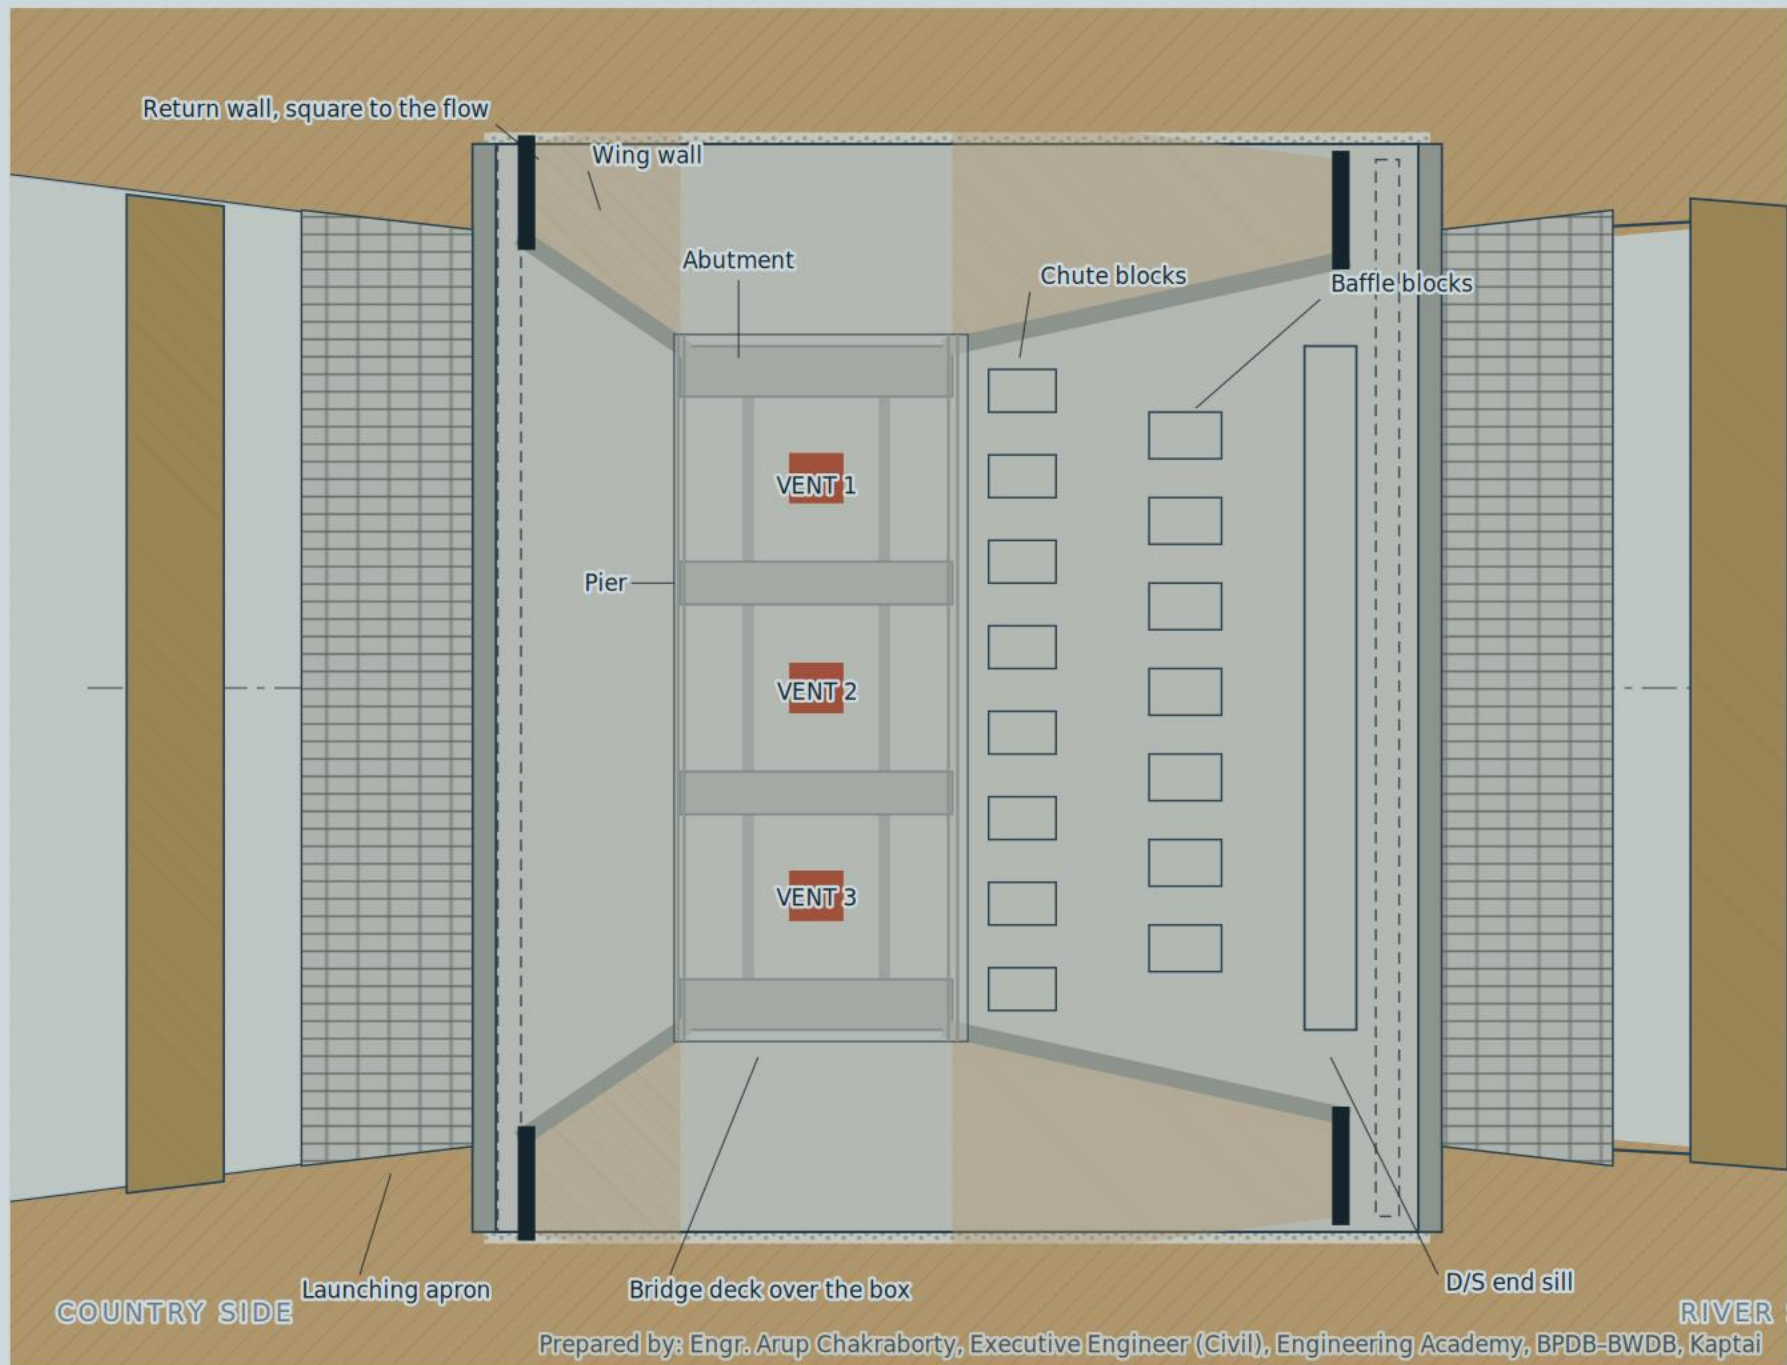

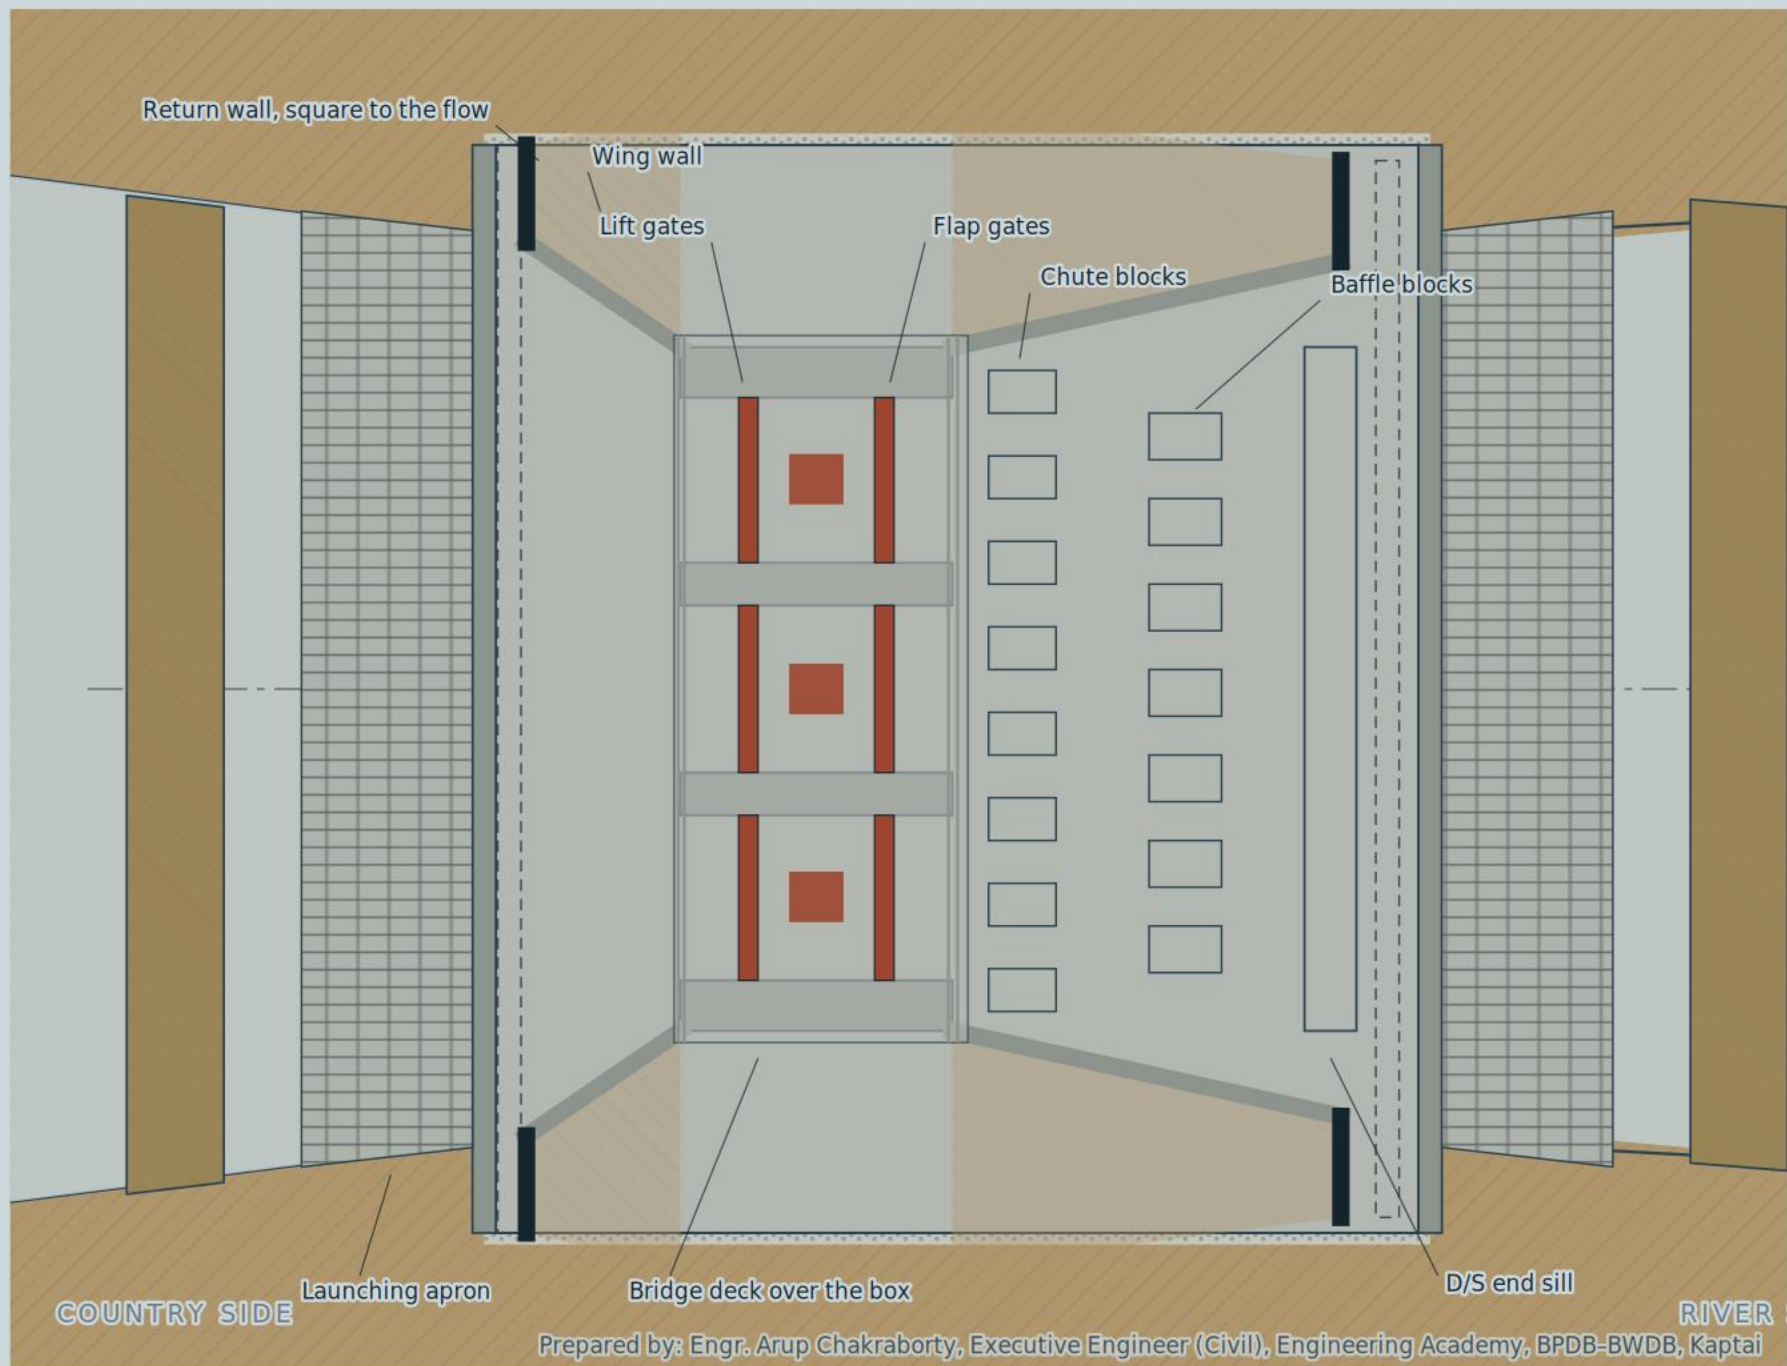

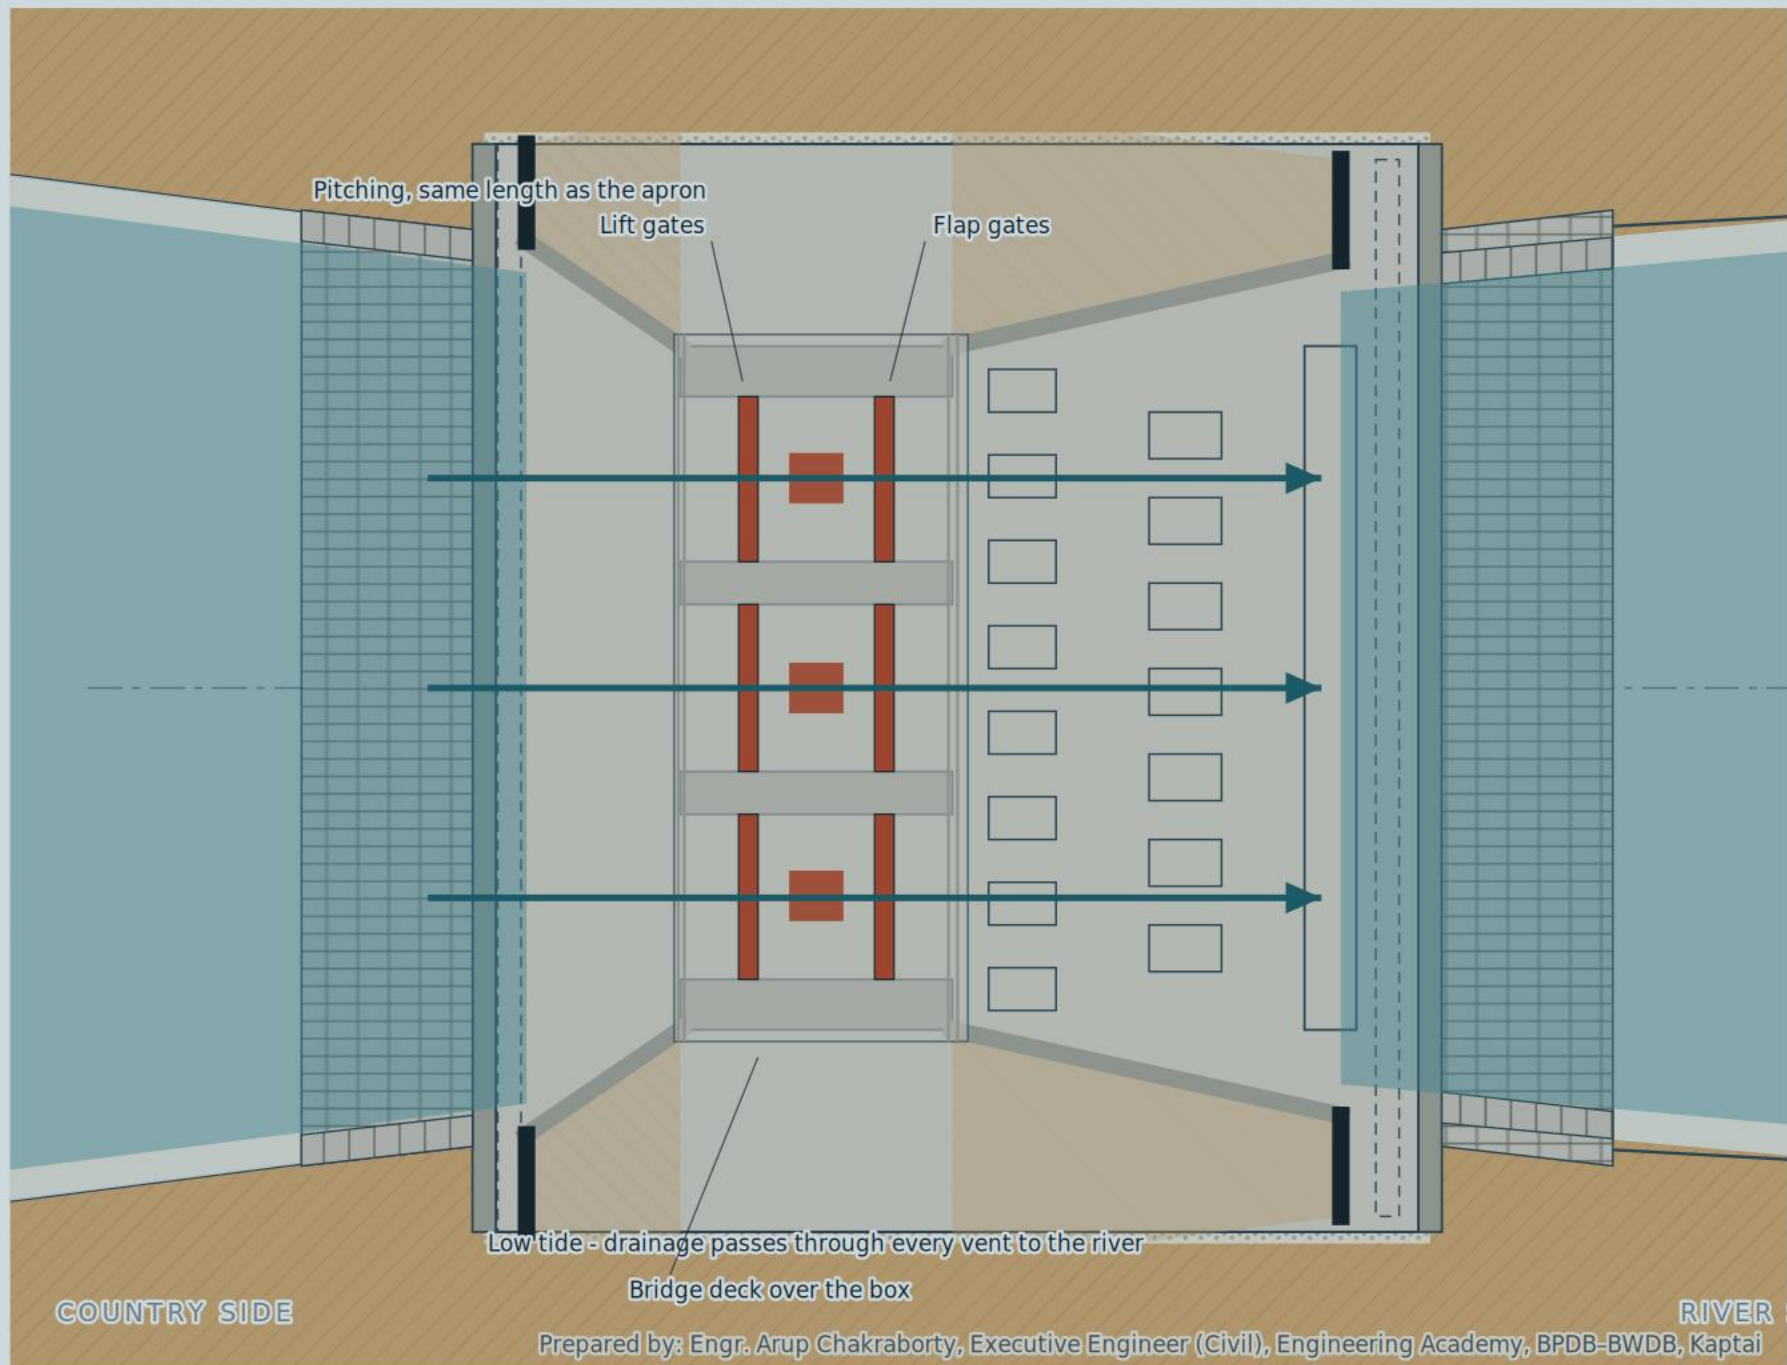

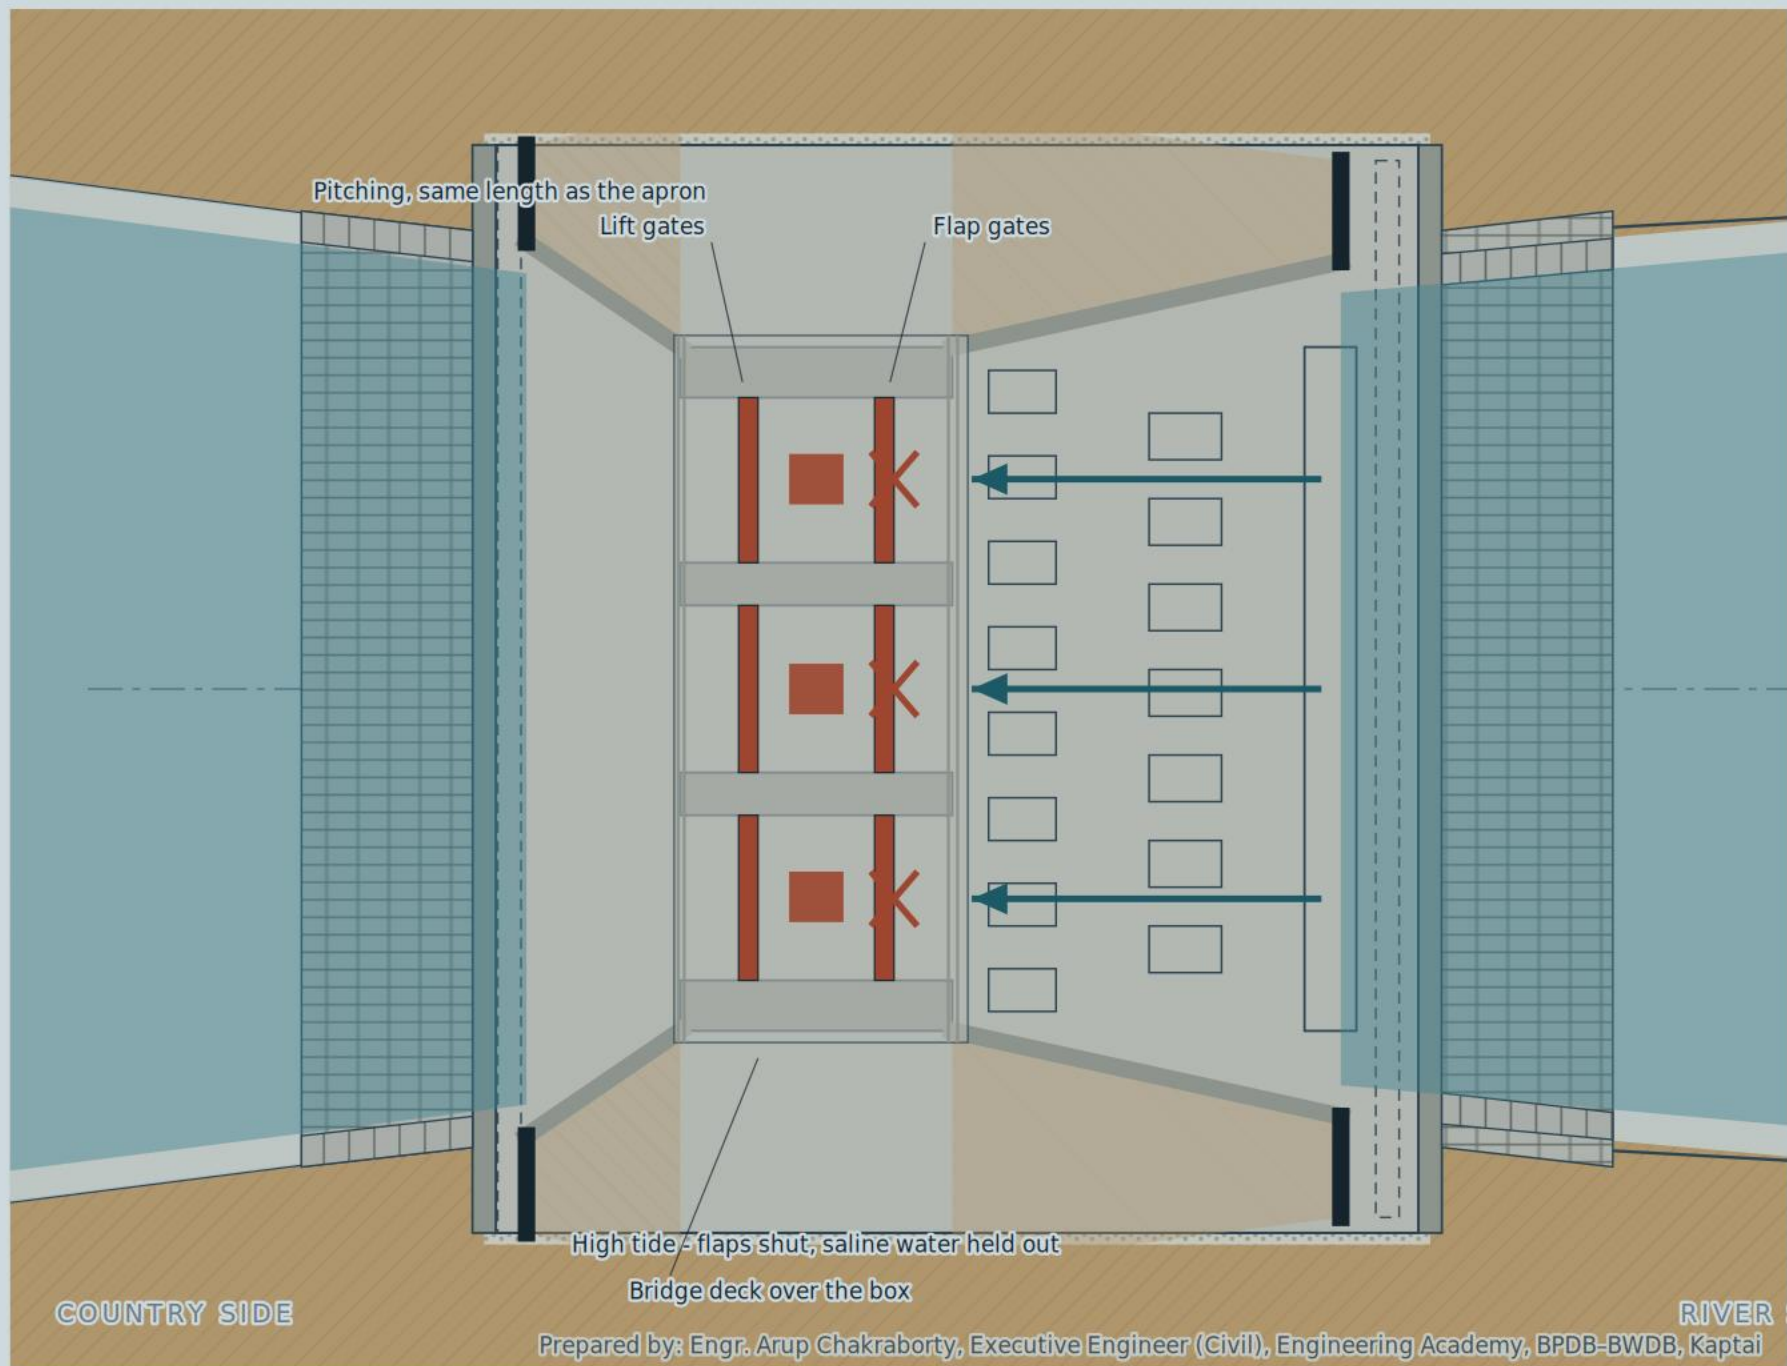


CENTRE LINE

VIEWED FROM THE RIVER SIDE




VIEWED FROM THE RIVER SIDE


CENTRE LINE

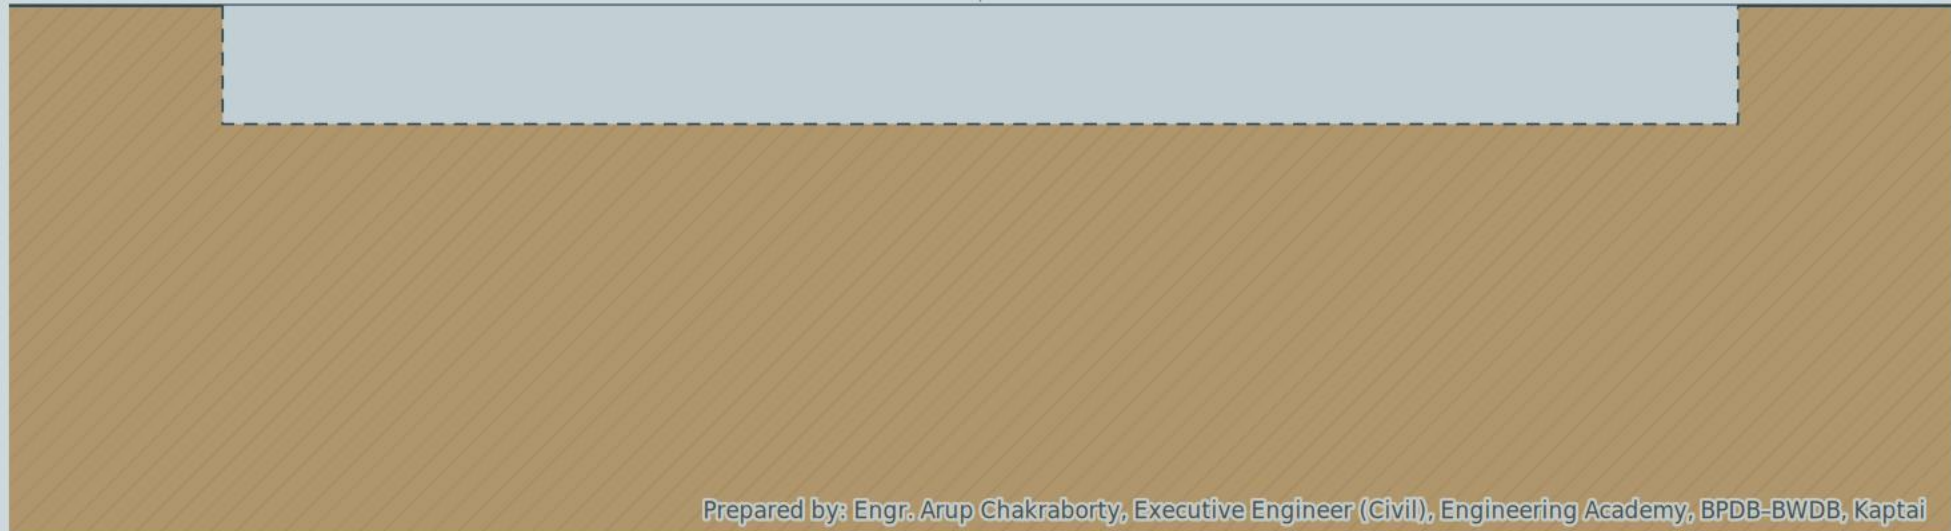



VIEWED FROM THE RIVER SIDE

CENTRE LINE

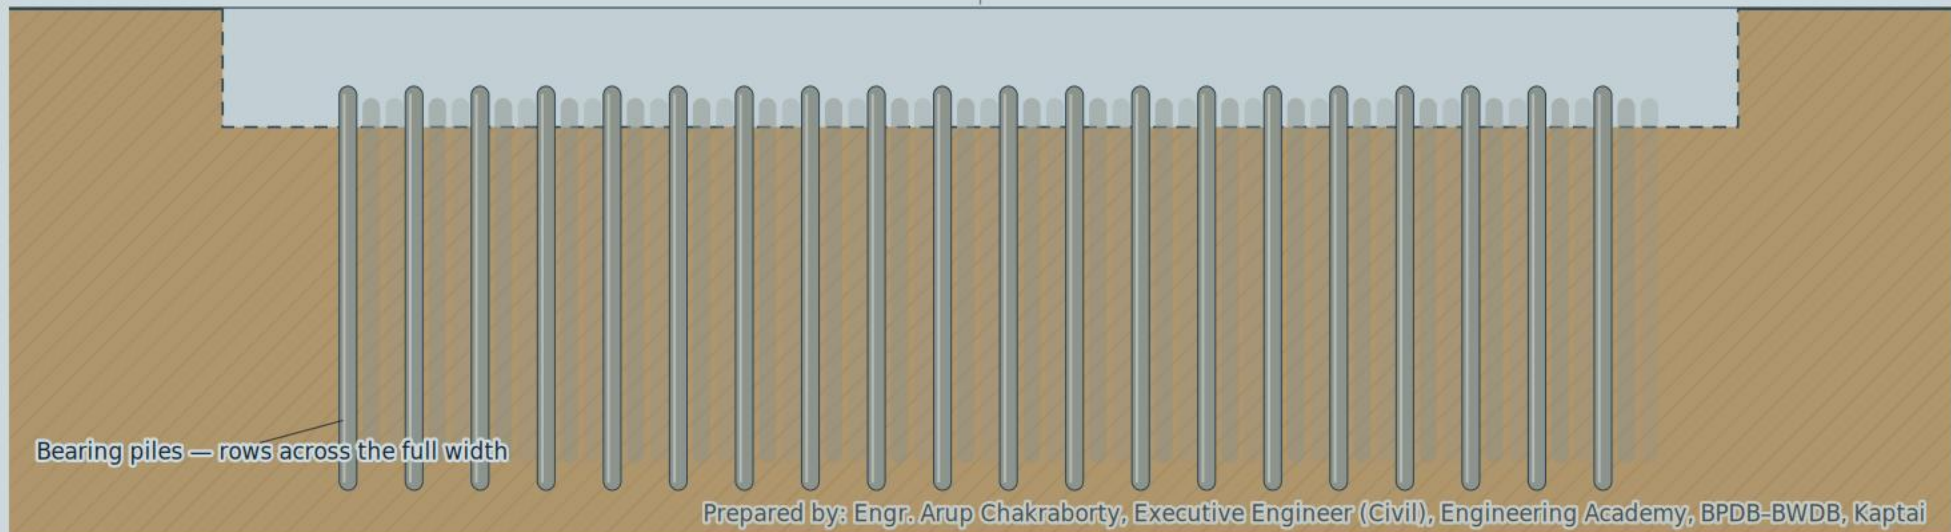

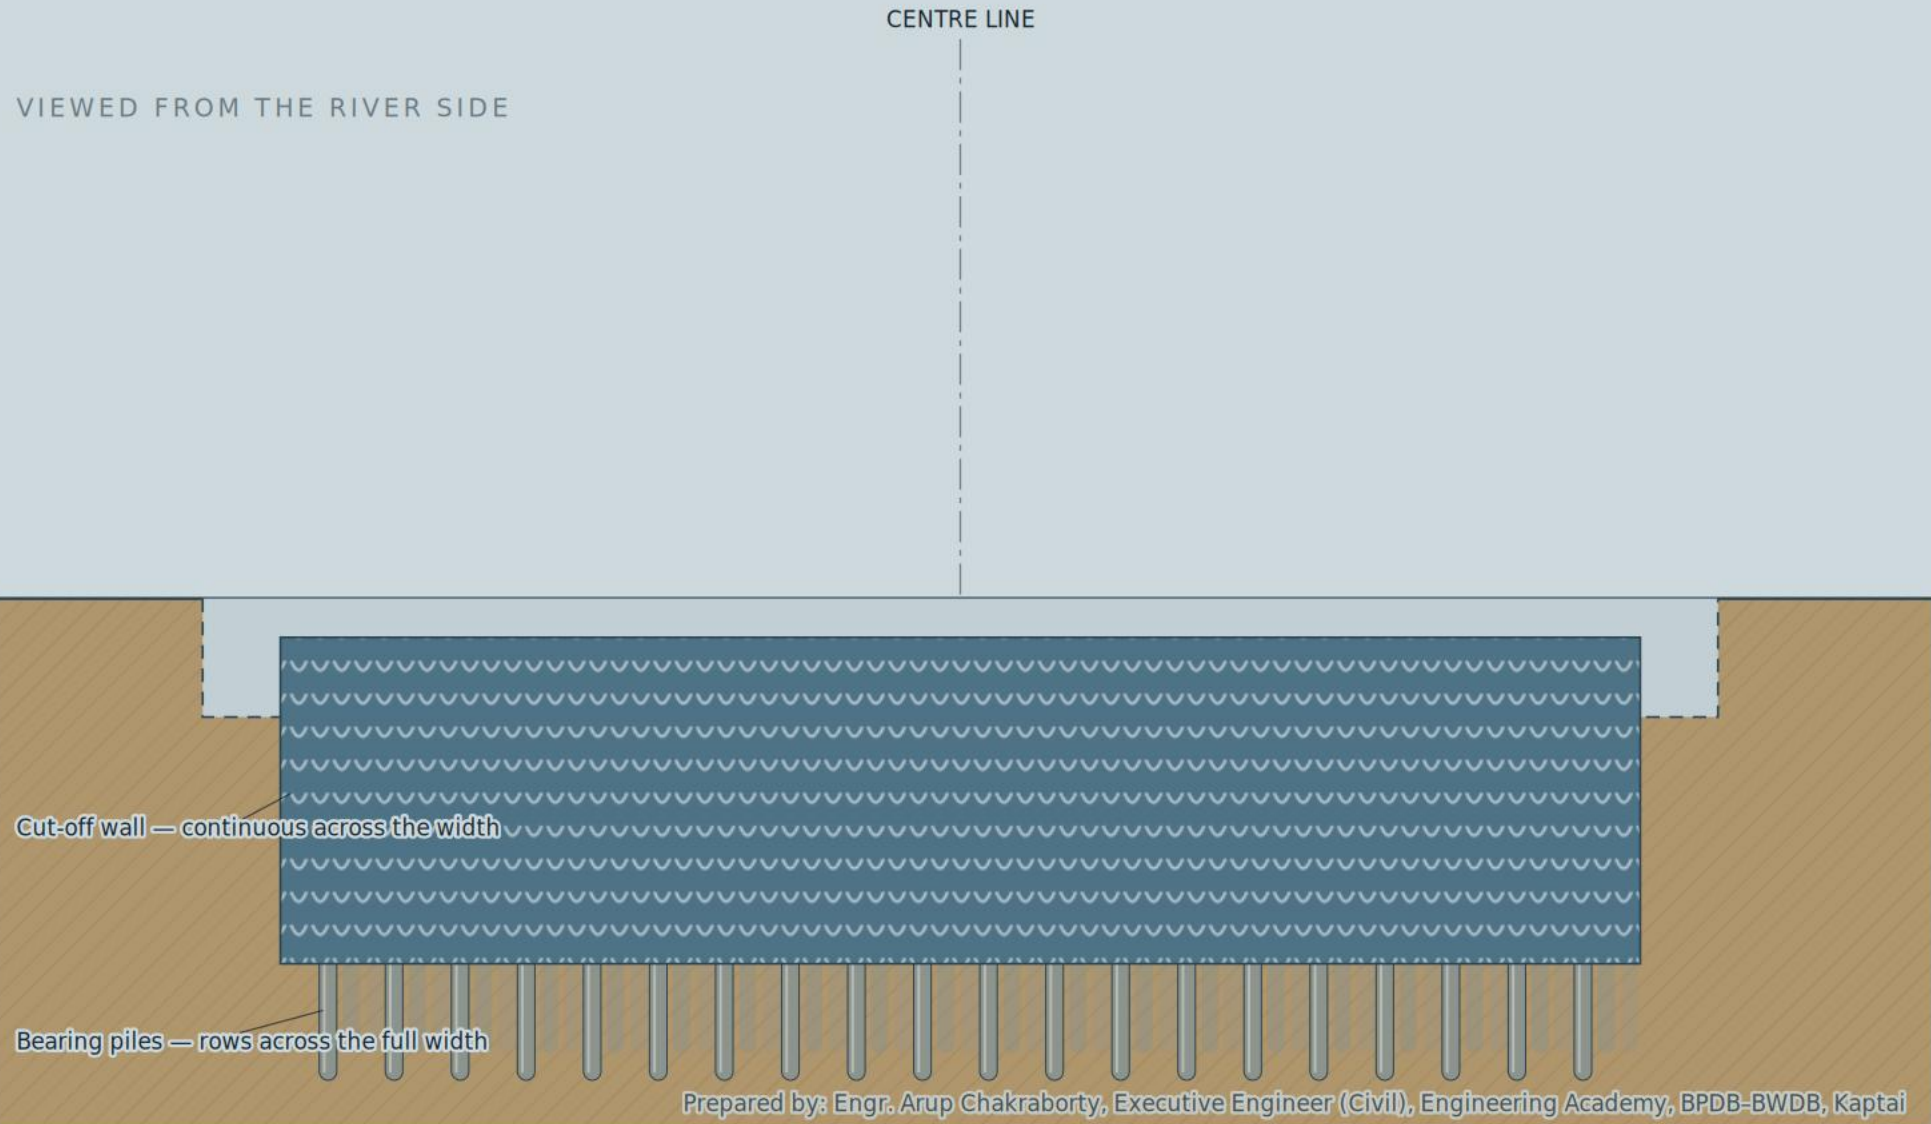


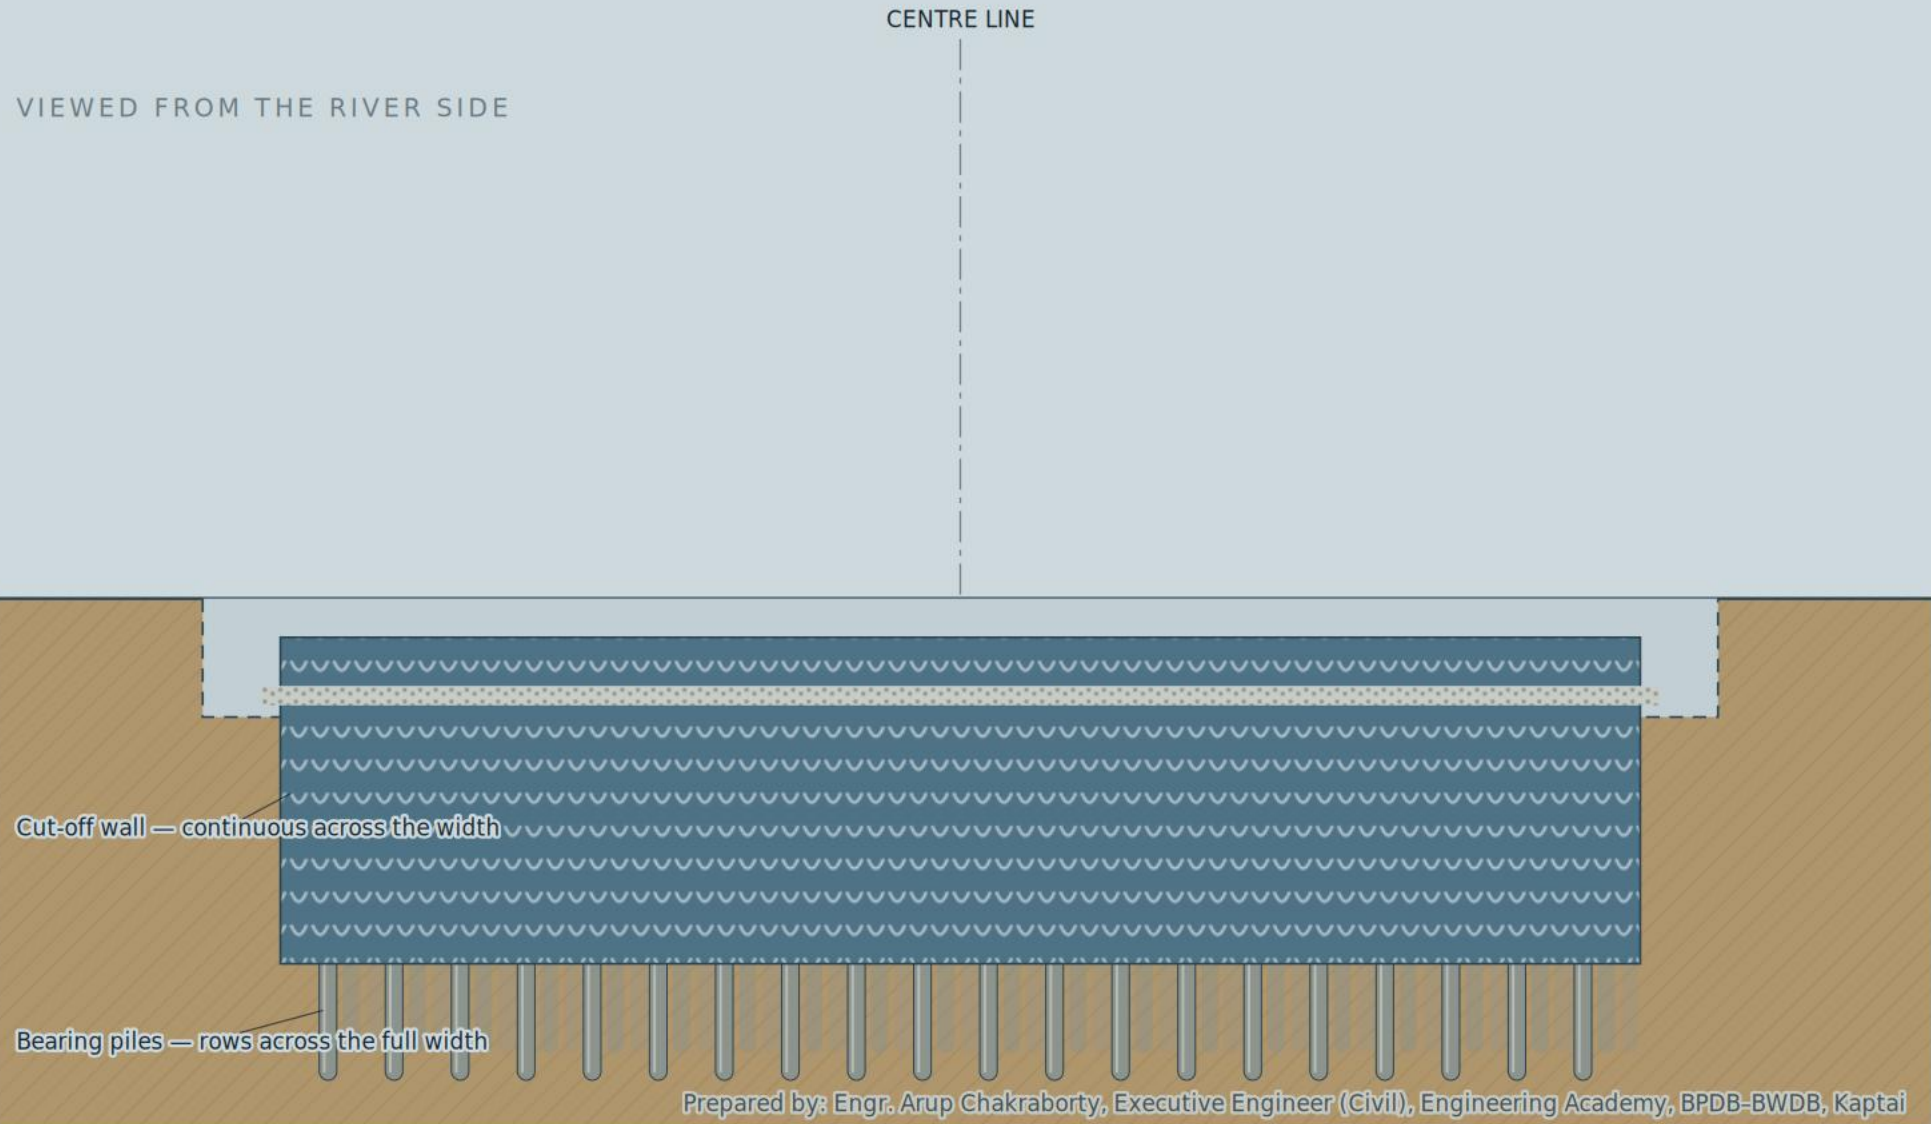


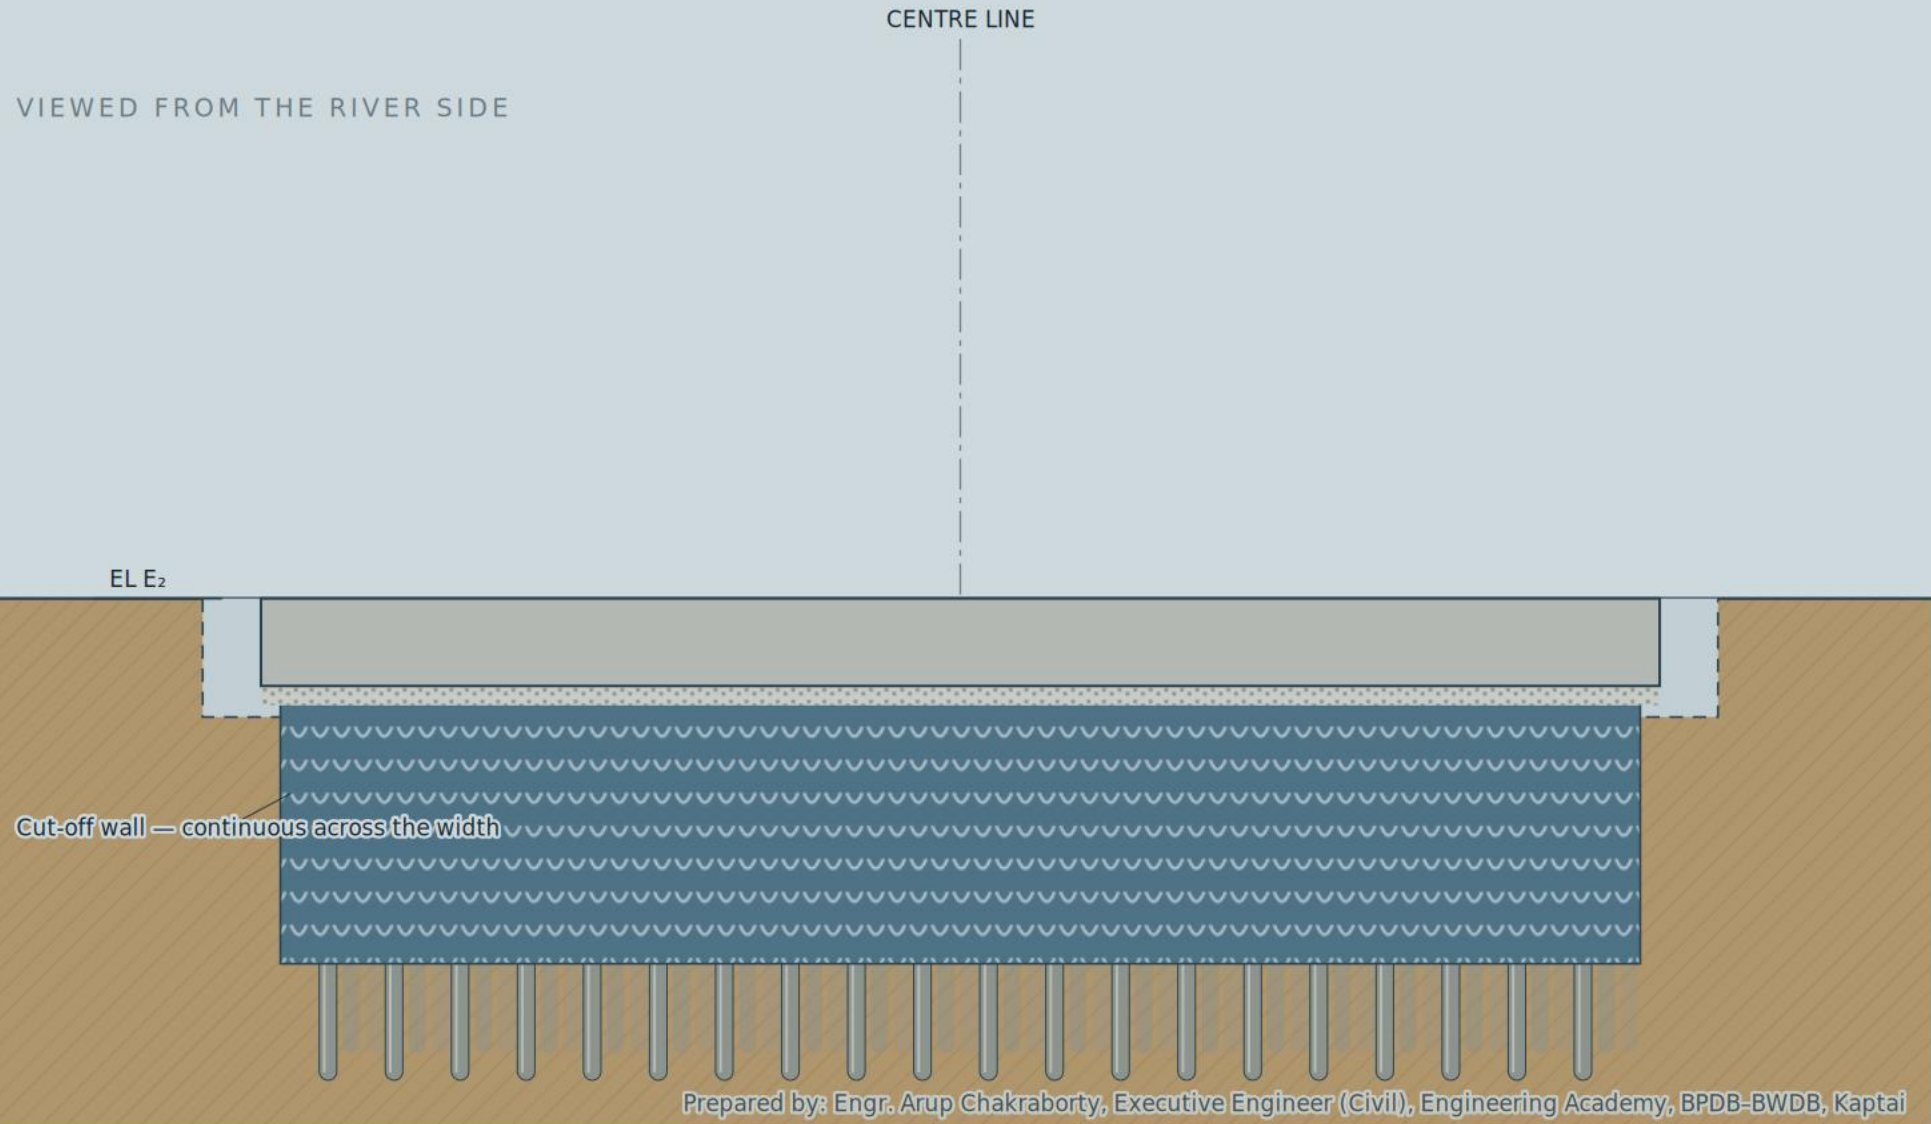






--	--

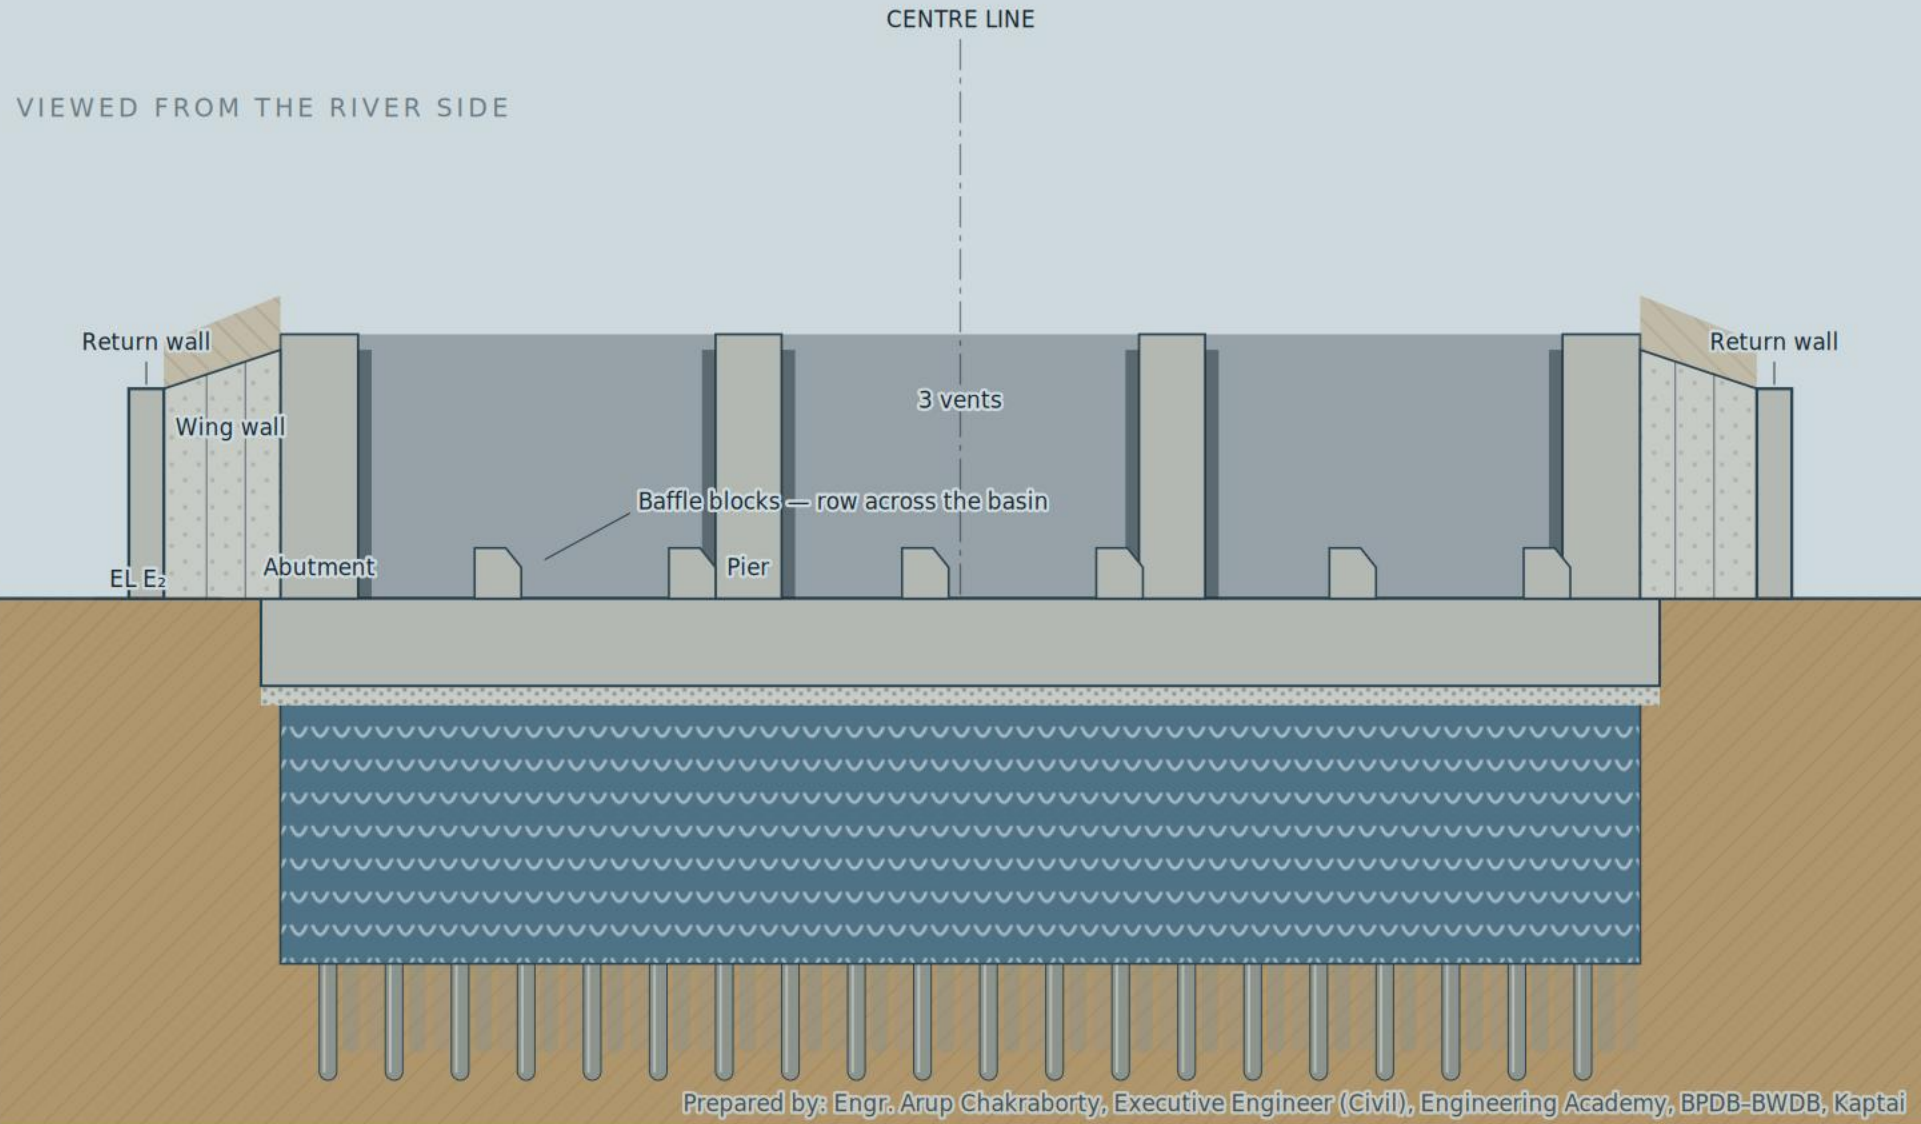

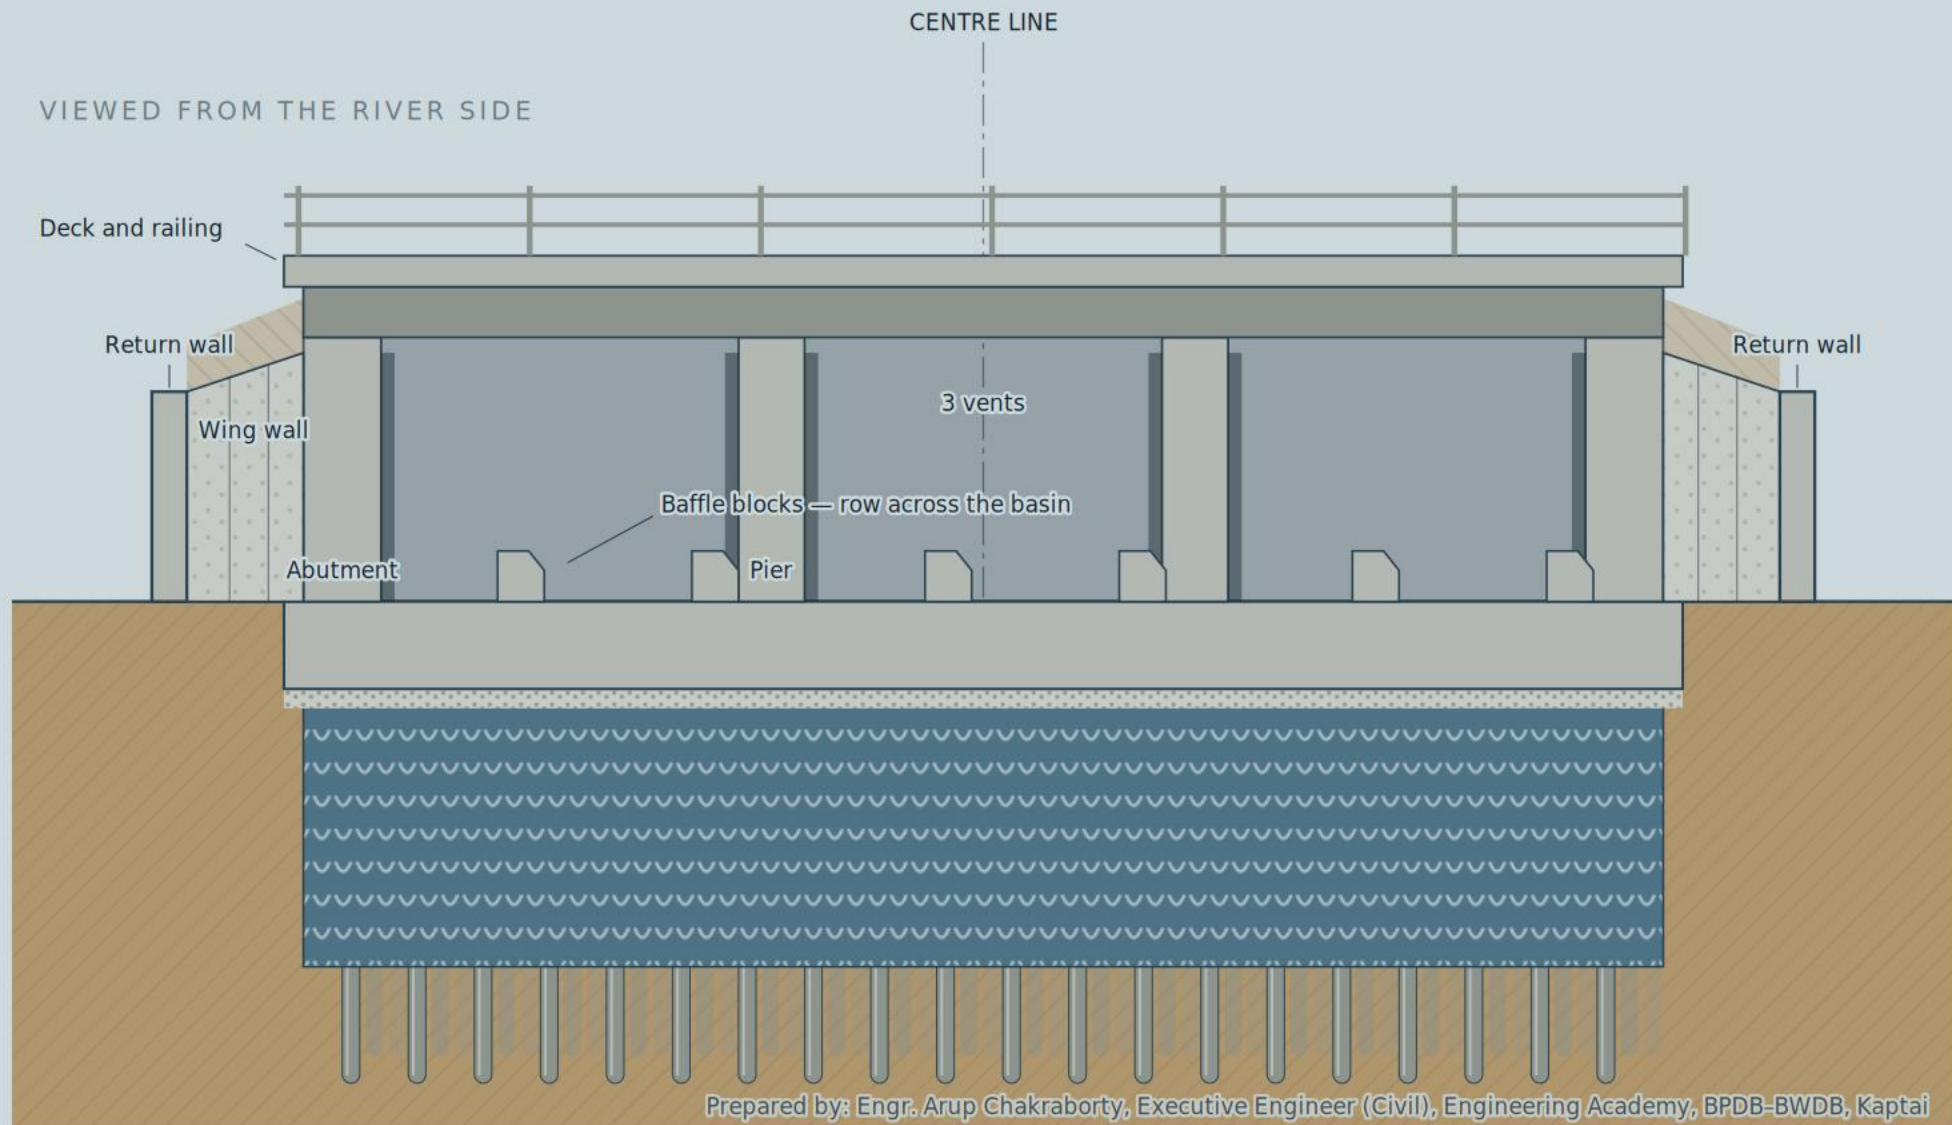

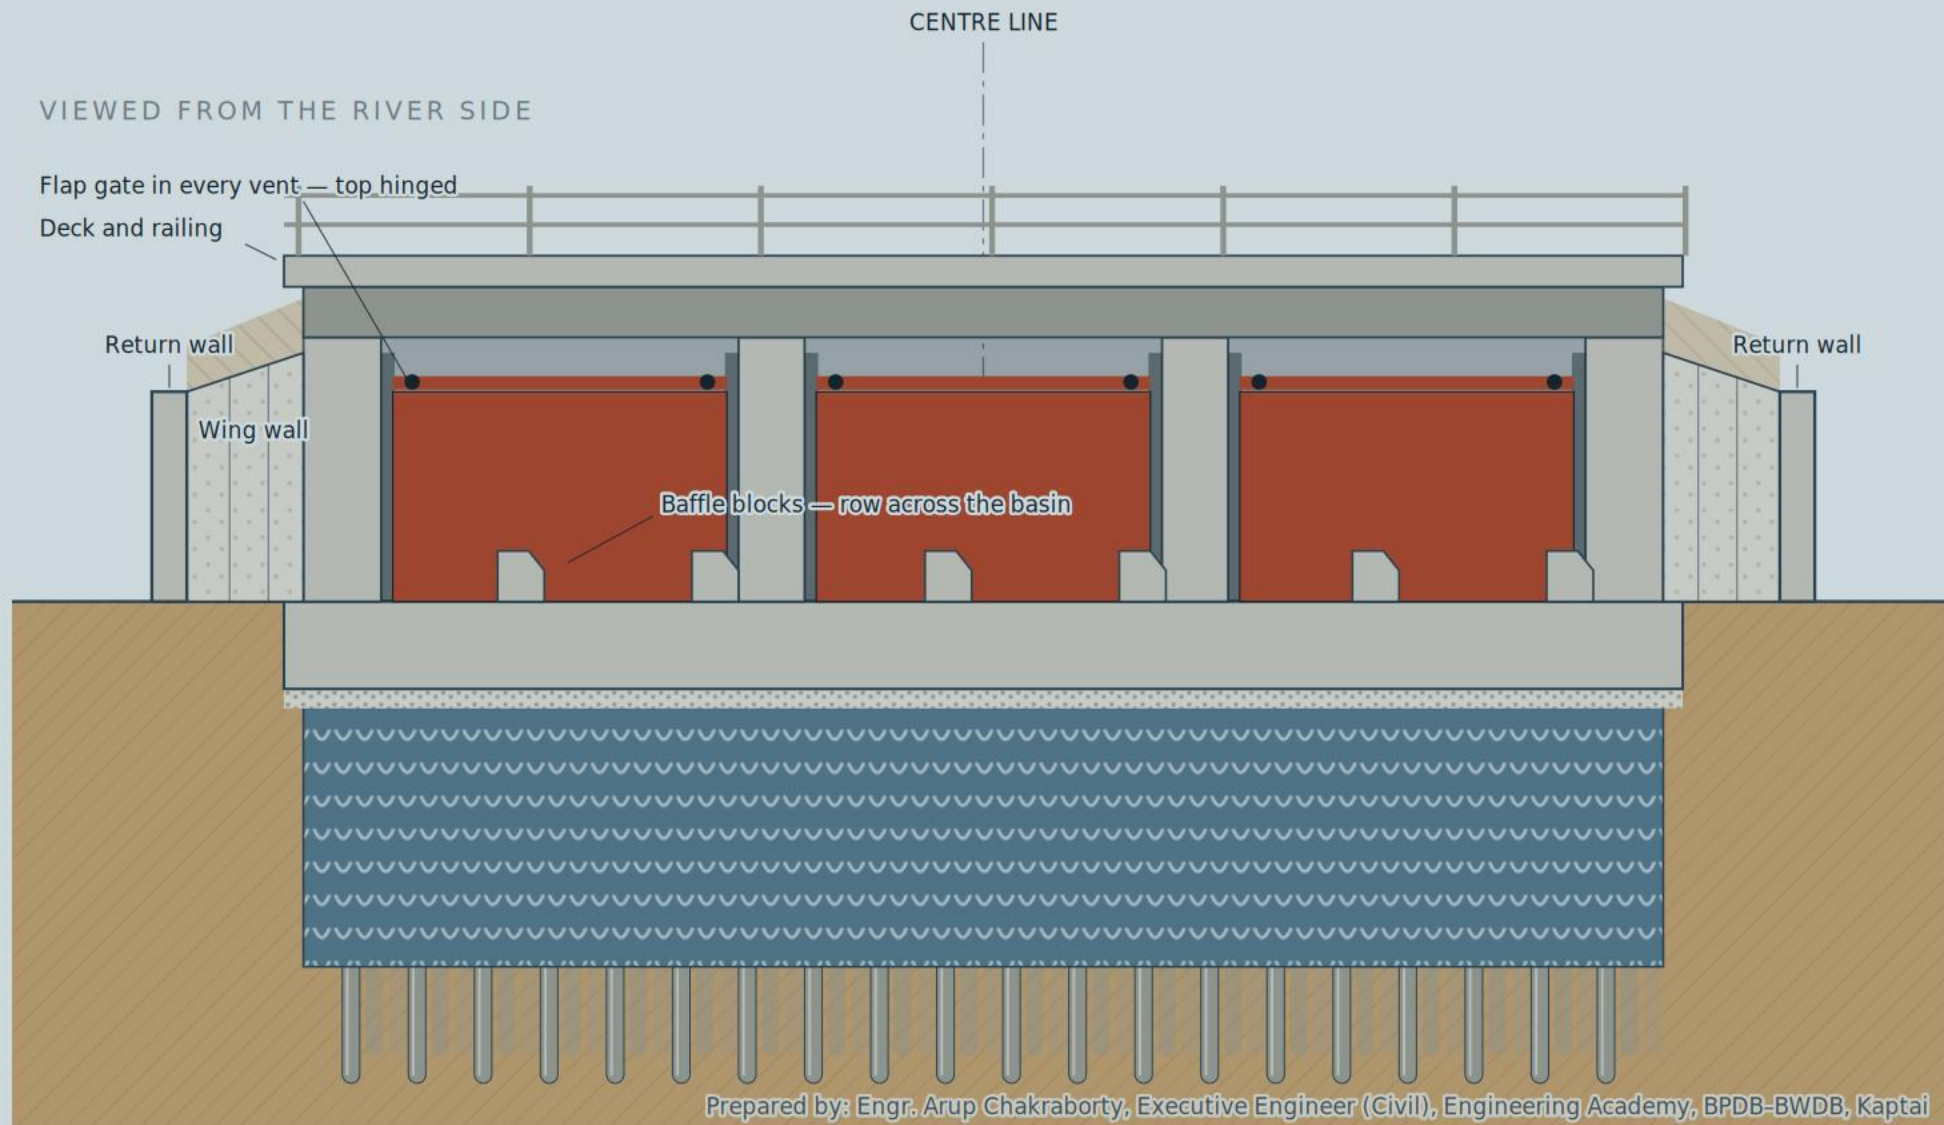

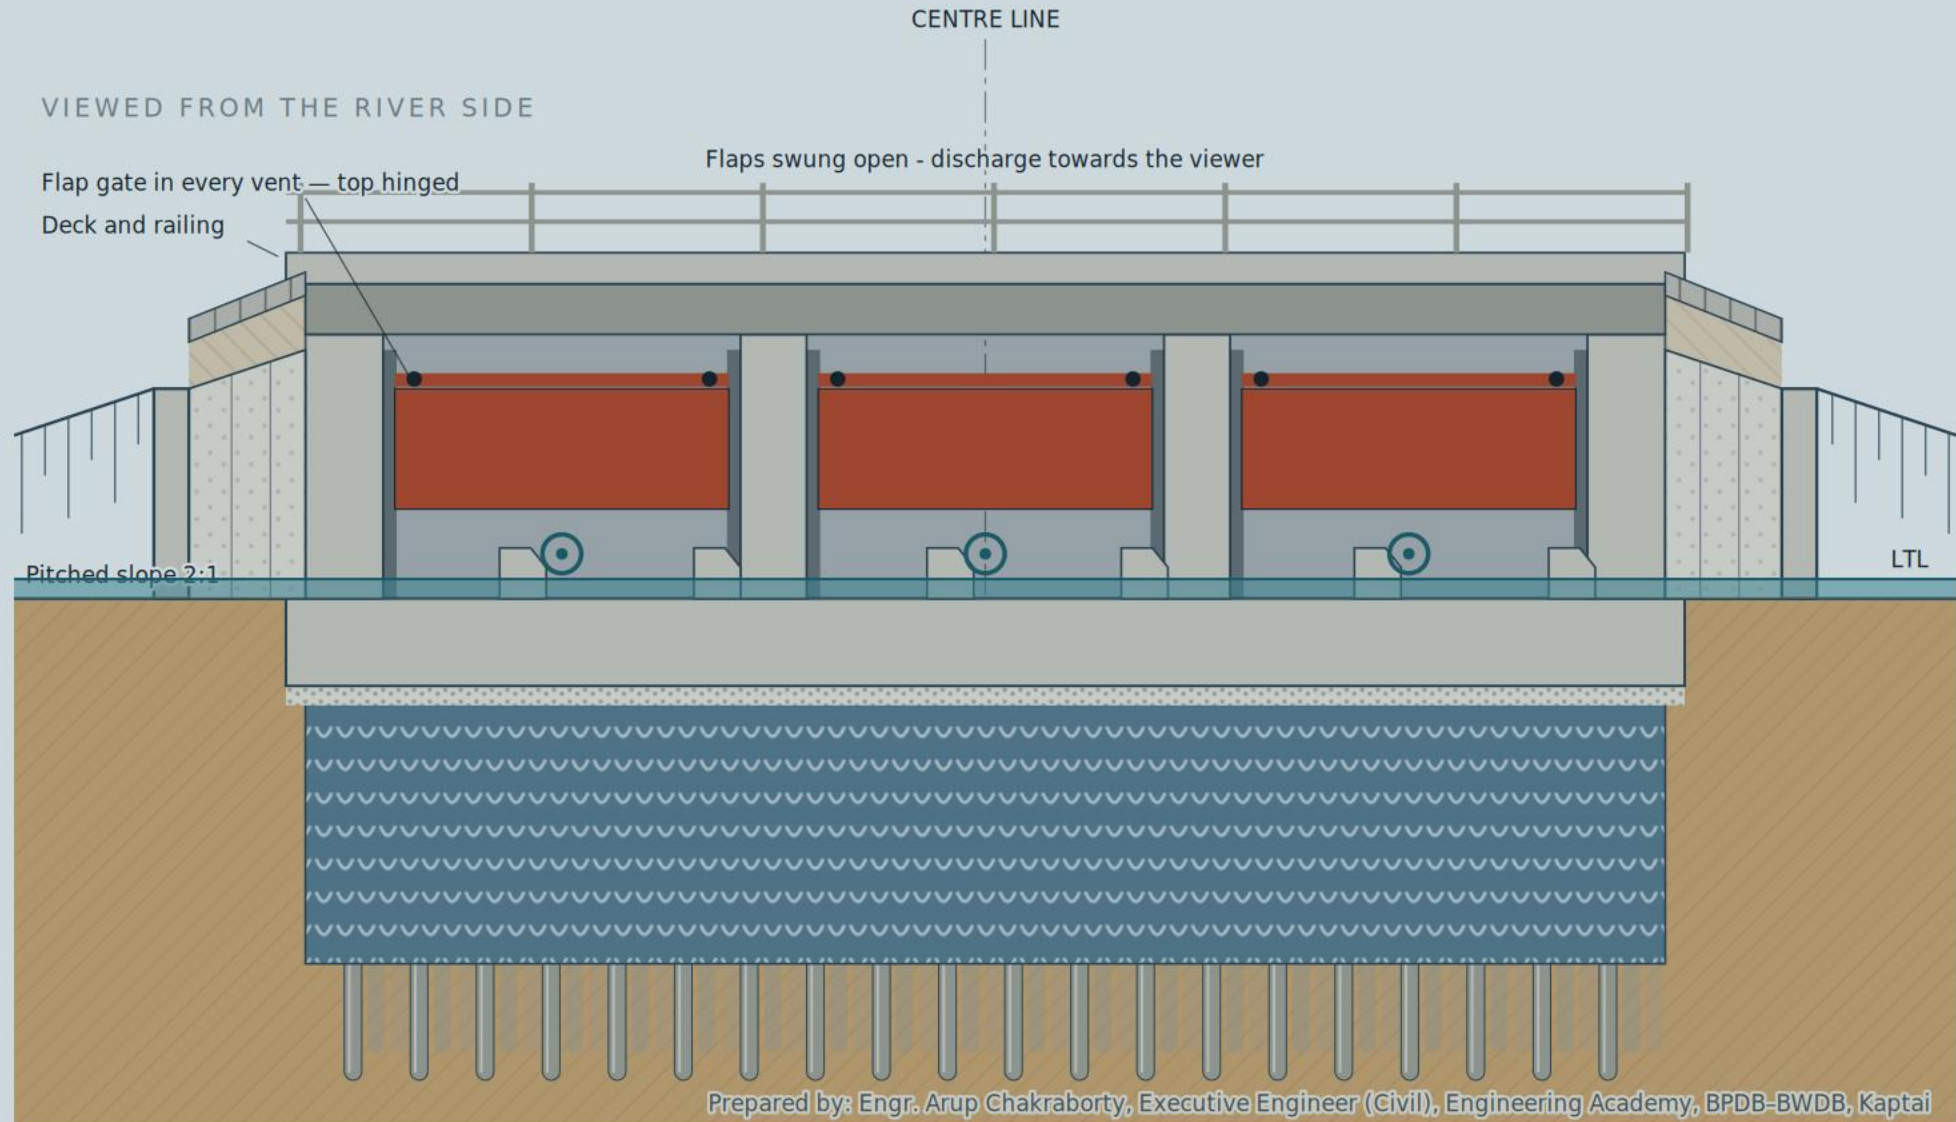

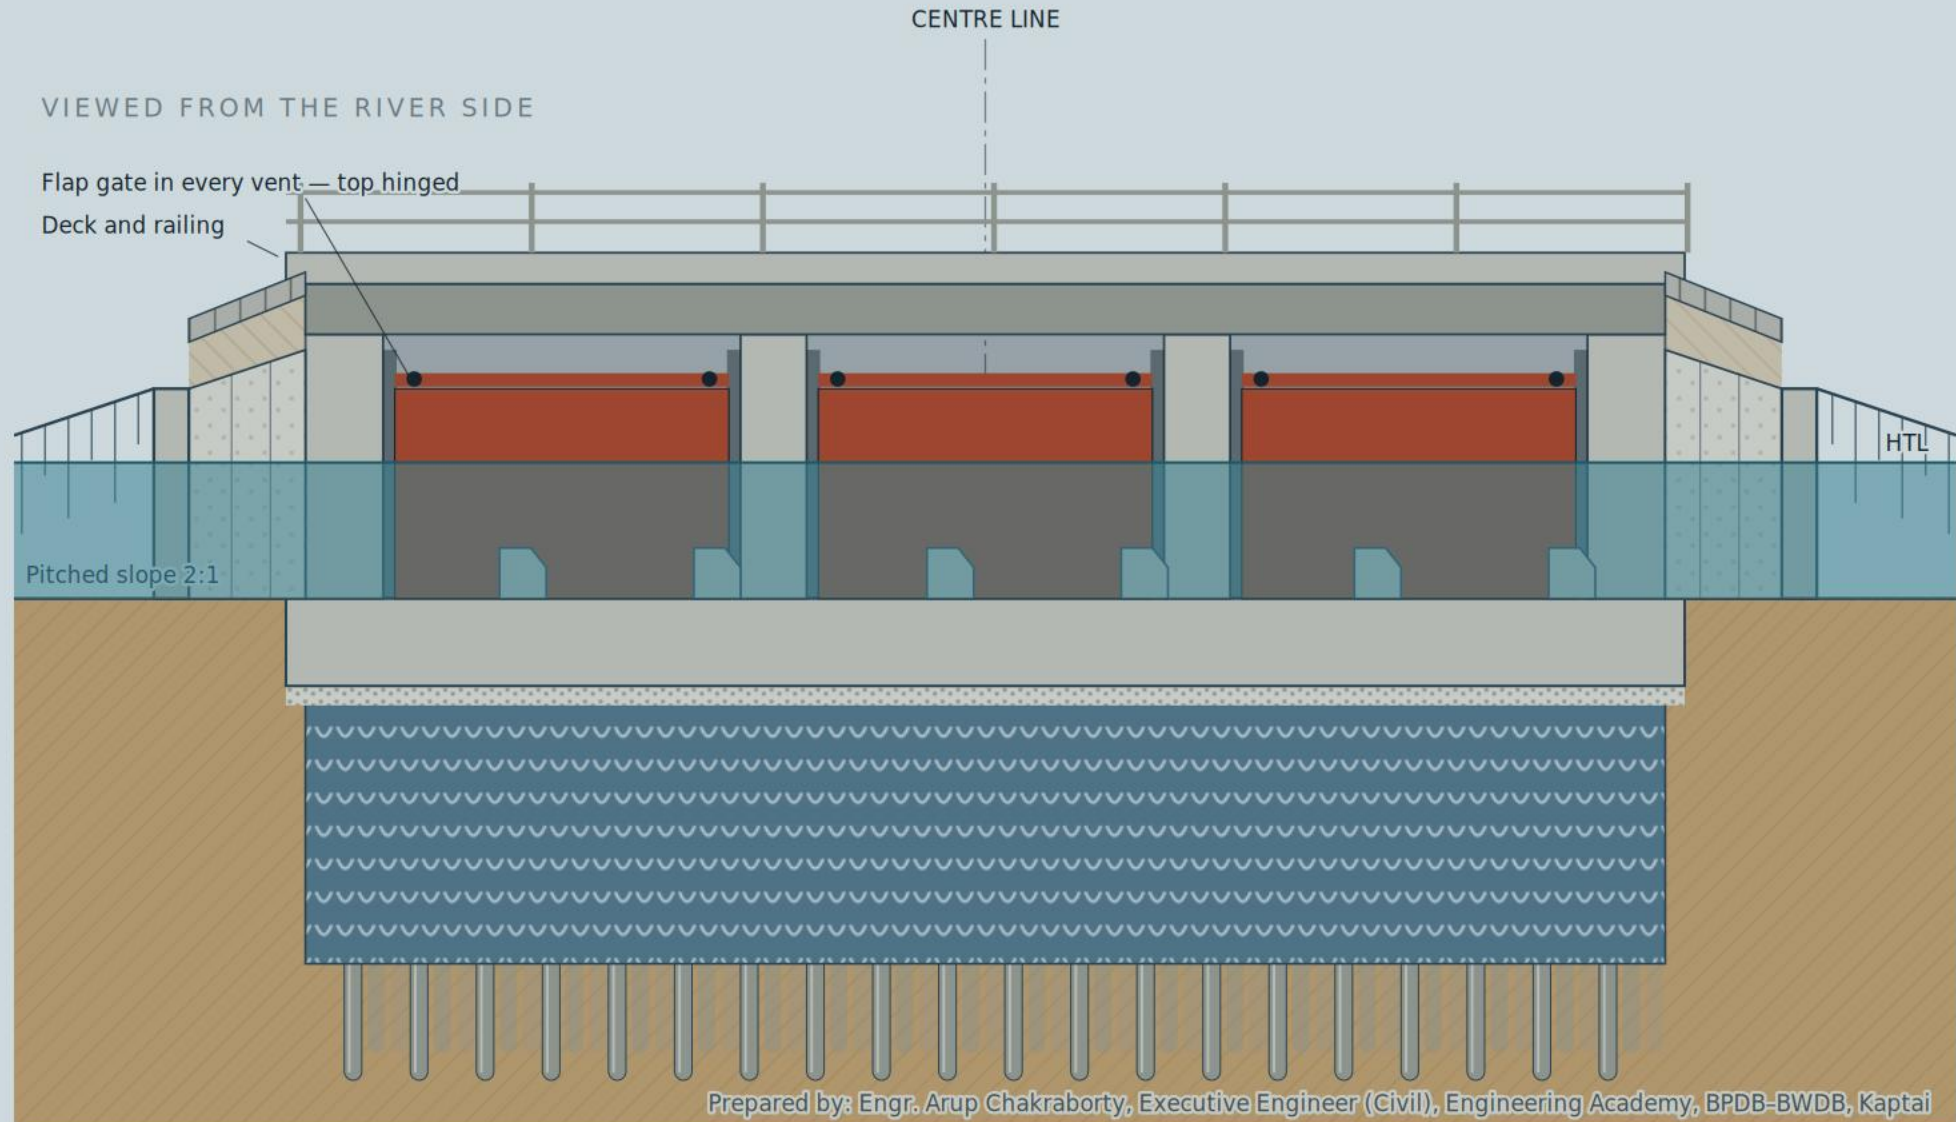

CENTRE LINE

VIEWED FROM THE COUNTRY SIDE



CENTRE LINE

VIEWED FROM THE COUNTRY SIDE



VIEWED FROM THE COUNTRY SIDE

CENTRE LINE

